
Jl. Betet

POTONGAN A-A' - EKSISTING

JL. BETET | SKALA 1:100

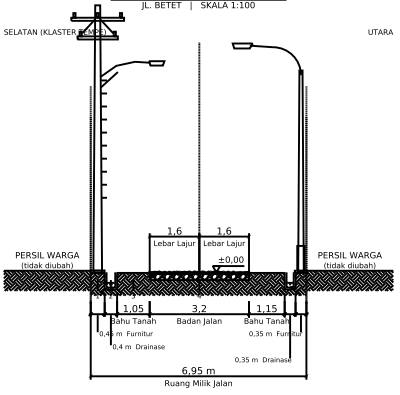


1. Tiang PJU / listrik eksisting
2. Saluran terbuka eksisting
3. Bahu tanah eksisting
4. Perkerasan aspal eksisting

Jl. Betet


POTONGAN A-A' - RENCANA

JL. BETET | SKALA 1:100

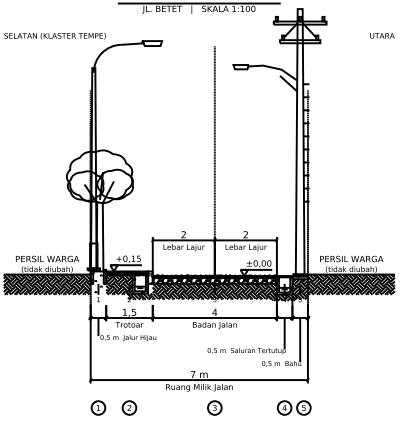

1. Jalur hijau: ketapang kencana + PJU
2. Paving block t=6 cm + pasir t=5 cm; Kanstin beton 15x40 cm (+0,15)
3. Perkerasan aspal AC-WC t=5 cm; Lapis pondasi agregat kelas A t=20 cm
4. Saluran U-ditch beton + tutup grill baja
5. Bahu beton t=10 cm

DENAH RUAS SEKITAR POTONGAN A | SKALA 1:200

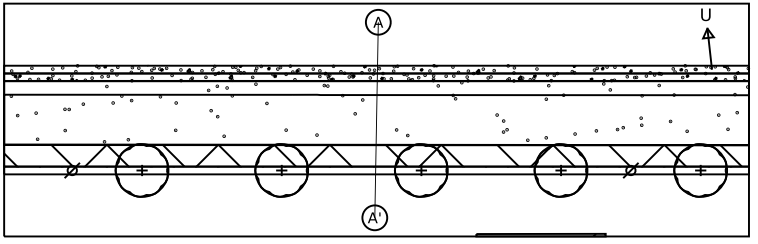

PENAMPANG JALAN PERMUKIMAN

KAWASAN PASAR INDUK KROYA

"KROYA SMART UNIFIED MARKET"


KEC. KROYA, KAB. CILACAP, JAWA TENGAH

POTONGAN A-A'

JL. BETET

EKSISTING (KIRI) & RENCANA (KANAN)

KEY PLAN

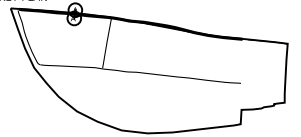

LEGENDA ARSIR

- Aspal AC-WC
- Agregat kelas A
- Beton (kanstin, U-ditch)
- Paving block trotoar
- Paving jalur sepeda
- Tanah dasar / urug
- Tanah taman / jalur hijau
- Tutup grill baja
- Batas ruang milik jalan / persil
- As jalan

CATATAN

1. Ukuran dalam meter; elevasi relatif terhadap muka aspal (±0,00).
2. Ruang milik jalan eksisting dipertahankan; rumah warga tidak dibongkar (Asistensi 4).
3. Ukuran eksisting: survei kelompok D3.2 & Andalalin 2023.
4. Skala 1:100 pada kertas A3.

STUDIO PERANCANGAN KOTA - KELOMPOK D3.2

Departemen Perencanaan Wilayah dan Kota


Dosen Pengampu: Novia Sari Ristianti, S.T., M.T.

SKALA	TANGGAL	LEMBAR
1 : 100 (A3)	28 Okt 2026	1 / 5

Jl. Cendrawasih

POTONGAN B1-B1' - EKSISTING

JL. CENDRAWASIH - SEGMEN PERMUKIMAN | SKALA 1:100

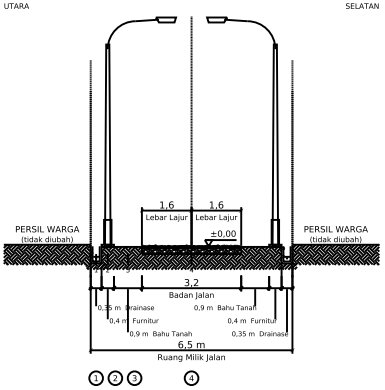


1. Saluran terbuka eksisting
2. Tiang PJU / listrik eksisting
3. Bahu tanah eksisting
4. Perkerasan aspal eksisting

Jl. Cendrawasih


POTONGAN B1-B1' - RENCANA

JL. CENDRAWASIH - SEGMEN PERMUKIMAN | SKALA 1:100

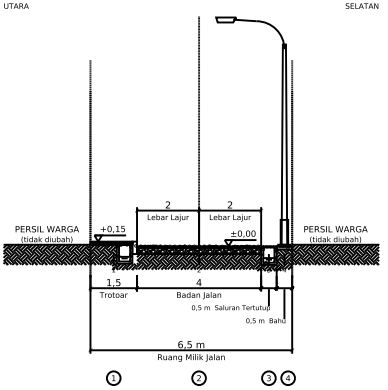

1. Paving block t=6 cm + pasir t=5 cm; Kanstin beton 15x40 cm (+0,15)
2. Perkerasan aspal AC-WC t=5 cm; Lapis pondasi agregat kelas A t=20 cm
3. Saluran U-ditch beton + tutup grill baja
4. Bahu beton t=10 cm

DENAH RUAS SEKITAR POTONGAN B1 | SKALA 1:200

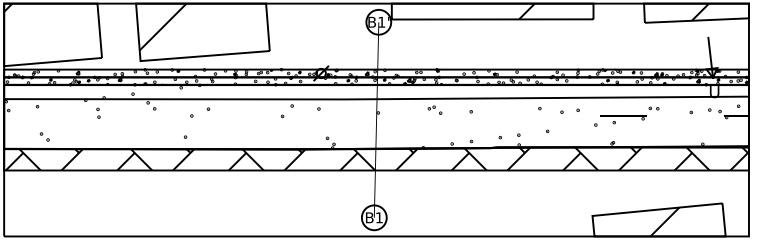

PENAMPANG JALAN PERMUKIMAN


KAWASAN PASAR INDUK KROYA
"KROYA SMART UNIFIED MARKET"
KEC. KROYA, KAB. CILACAP, JAWA TENGAH

POTONGAN B1-B1'

JL. CENDRAWASIH - SEGMEN PERMUKIMAN

EKSISTING (KIRI) & RENCANA (KANAN)

KEY PLAN

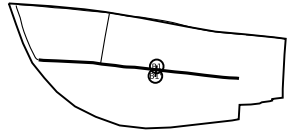

LEGENDA ARSIR

- Aspal AC-WC
- Agregat kelas A
- Beton (kanstin, U-ditch)
- Paving block trotoar
- Paving jalur sepeda
- Tanah dasar / urug
- Tanah taman / jalur hijau
- Tutup grill baja
- Batas ruang milik jalan / persil
- As jalan

CATATAN

1. Ukuran dalam meter; elevasi relatif terhadap muka aspal (±0,00).
2. Ruang milik jalan eksisting dipertahankan; rumah warga tidak dibongkar (Asistensi 4).
3. Ukuran eksisting: survei kelompok D3.2 & Andalalin 2023.
4. Skala 1:100 pada kertas A3.


STUDIO PERANCANGAN KOTA - KELOMPOK D3.2
Departemen Perencanaan Wilayah dan Kota
Dosen Pengampu: Novia Sari Ristianti, S.T., M.T.

SKALA	TANGGAL	LEMBAR
1 : 100 (A3)	28 Okt 2026	2 / 5

Jl. Cendrawasih

POTONGAN B2-B2' - EKSISTING

JL. CENDRAWASIH - SEGMEN TEPI REL | SKALA 1:100

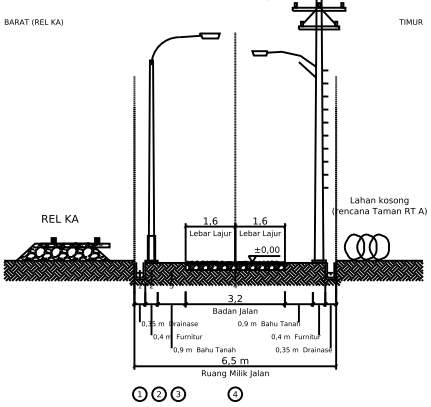


1. Saluran terbuka eksisting
2. Tiang PJU / listrik eksisting
3. Bahu tanah eksisting
4. Perkerasan aspal eksisting

Jl. Cendrawasih


POTONGAN B2-B2' - RENCANA

JL. CENDRAWASIH - SEGMEN TEPI REL | SKALA 1:100

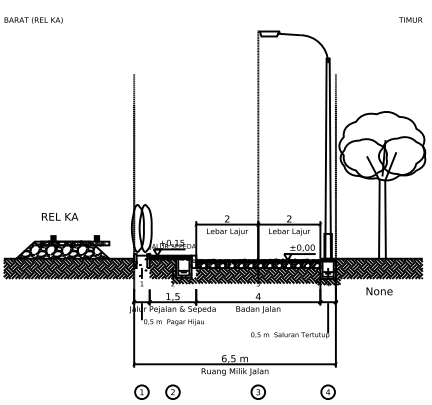

1. Pagar hijau perdu h=1,5 m (bambu pagar / teh-tehan)
2. Jalur pejalan & sepeda: paving t=6 cm; marka sepeda, kanstin beton 15x40 cm
3. Perkerasan aspal AC-WC t=5 cm; Lapis pondasi agregat kelas A t=20 cm
4. Saluran U-ditch beton + tutup grill baja

DENAH RUAS SEKITAR POTONGAN B2 | SKALA 1:200

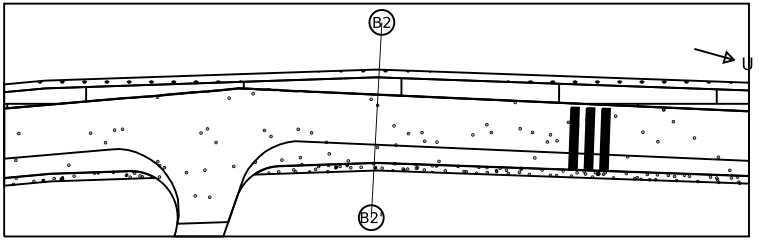

PENAMPANG JALAN PERMUKIMAN

KAWASAN PASAR INDUK KROYA

"KROYA SMART UNIFIED MARKET"


KEC. KROYA, KAB. CILACAP, JAWA TENGAH

POTONGAN B2-B2'

JL. CENDRAWASIH - SEGMEN TEPI REL

EKSISTING (KIRI) & RENCANA (KANAN)

KEY PLAN

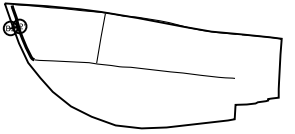

LEGENDA ARSIR

- Aspal AC-WC
- Agregat kelas A
- Beton (kanstin, U-ditch)
- Paving block trotoar
- Paving jalur sepeda
- Tanah dasar / urug
- Tanah taman / jalur hijau
- Tutup grill baja
- Batas ruang milik jalan / persil
- As jalan

CATATAN

1. Ukuran dalam meter; elevasi relatif terhadap muka aspal (±0,00).
2. Ruang milik jalan eksisting dipertahankan; rumah warga tidak dibongkar (Asistensi 4).
3. Ukuran eksisting: survei kelompok D3.2 & Andalalin 2023.
4. Skala 1:100 pada kertas A3.

STUDIO PERANCANGAN KOTA - KELOMPOK D3.2

Departemen Perencanaan Wilayah dan Kota


Dosen Pengampu: Novia Sari Ristianti, S.T., M.T.

SKALA	TANGGAL	LEMBAR
1 : 100 (A3)	28 Okt 2026	3 / 5

Jl. Letkol Sudarso

POTONGAN C-C' - EKSISTING

JL. LETKOL SUDARSO | SKALA 1:100

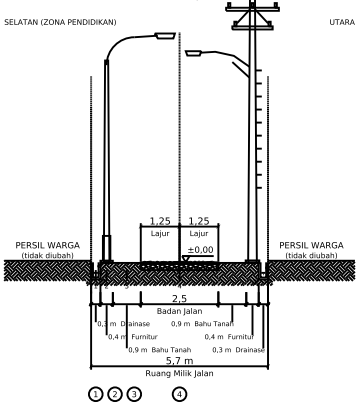


1. Saluran terbuka eksisting
2. Tiang PJU / listrik eksisting
3. Bahu tanah eksisting
4. Perkerasan aspal eksisting

Jl. Letkol Sudarso


POTONGAN C-C' - RENCANA

JL. LETKOL SUDARSO | SKALA 1:100

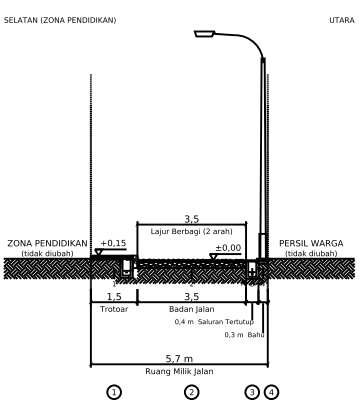

1. Paving block t=6 cm + pasir t=5 cm; Kanstin beton 15x40 cm (+0,15)
2. Perkerasan aspal AC-WC t=5 cm; Lapis pondasi agregat kelas A t=20 cm
3. Saluran U-ditch beton + tutup grill baja
4. Bahu beton t=10 cm

DENAH RUAS SEKITAR POTONGAN C | SKALA 1:200

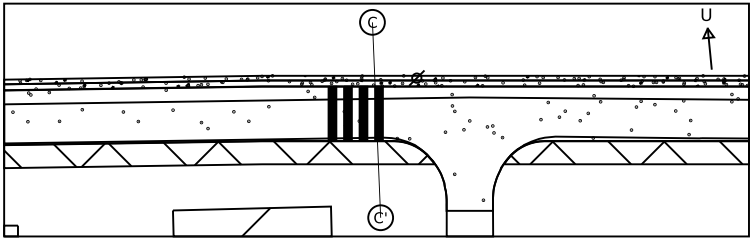

PENAMPANG JALAN PERMUKIMAN

KAWASAN PASAR INDUK KROYA

"KROYA SMART UNIFIED MARKET"


KEC. KROYA, KAB. CILACAP, JAWA TENGAH

POTONGAN C-C'

JL. LETKOL SUDARSO

EKSISTING (KIRI) & RENCANA (KANAN)

KEY PLAN

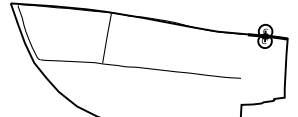

LEGENDA ARSIR

- Aspal AC-WC
- Agregat kelas A
- Beton (kanstin, U-ditch)
- Paving block trotoar
- Paving jalur sepeda
- Tanah dasar / urug
- Tanah taman / jalur hijau
- Tutup grill baja
- Batas ruang milik jalan / persil
- As jalan

CATATAN

1. Ukuran dalam meter; elevasi relatif terhadap muka aspal (±0,00).
2. Ruang milik jalan eksisting dipertahankan; rumah warga tidak dibongkar (Asistensi 4).
3. Ukuran eksisting: survei kelompok D3.2 & Andalalin 2023.
4. Skala 1:100 pada kertas A3.

STUDIO PERANCANGAN KOTA - KELOMPOK D3.2

Departemen Perencanaan Wilayah dan Kota


Dosen Pengampu: Novia Sari Ristianti, S.T., M.T.

SKALA	TANGGAL	LEMBAR
1 : 100 (A3)	28 Okt 2026	4 / 5

Jl. Ampas Waras

POTONGAN D-D' - EKSISTING

JL. AMPAS WARAS - DEPAN BALAI UMKM | SKALA 1:100

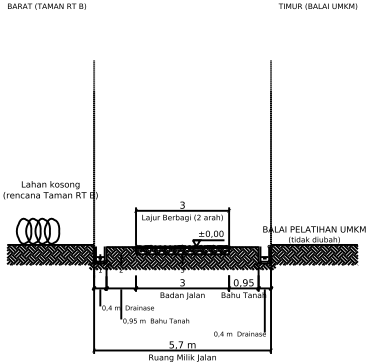


1. Saluran terbuka eksisting
2. Bahu tanah eksisting
3. Perkerasan aspal eksisting

Jl. Ampas Waras


POTONGAN D-D' - RENCANA

JL. AMPAS WARAS - DEPAN BALAI UMKM | SKALA 1:100

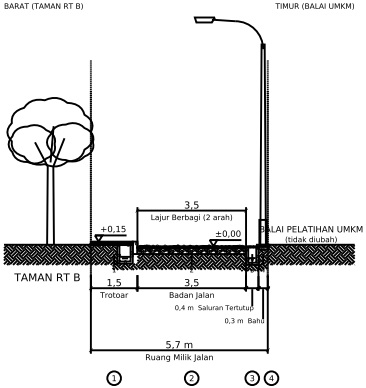

1. Paving block t=6 cm + pasir t=5 cm; Kanstin beton 15x40 cm (+0,15)
2. Perkerasan aspal AC-WC t=5 cm; Lapis pondasi agregat kelas A t=20 cm
3. Saluran U-ditch beton + tutup grill baja
4. Bahu beton t=10 cm

DENAH RUAS SEKITAR POTONGAN D | SKALA 1:200

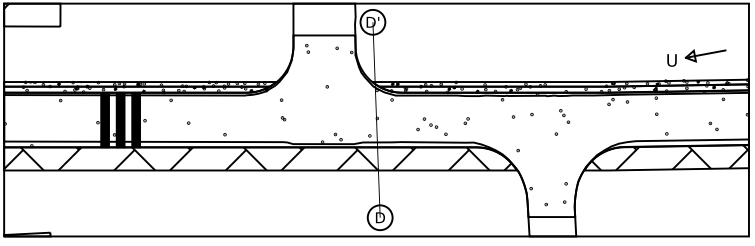

PENAMPANG JALAN PERMUKIMAN

KAWASAN PASAR INDUK KROYA

"KROYA SMART UNIFIED MARKET"


KEC. KROYA, KAB. CILACAP, JAWA TENGAH

POTONGAN D-D'

JL. AMPAS WARAS - DEPAN BALAI UMKM

EKSISTING (KIRI) & RENCANA (KANAN)

KEY PLAN

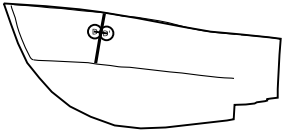

LEGENDA ARSIR

- Aspal AC-WC
- Agregat kelas A
- Beton (kanstin, U-ditch)
- Paving block trotoar
- Paving jalur sepeda
- Tanah dasar / urug
- Tanah taman / jalur hijau
- Tutup grill baja
- Batas ruang milik jalan / persil
- As jalan

CATATAN

1. Ukuran dalam meter; elevasi relatif terhadap muka aspal (±0,00).
2. Ruang milik jalan eksisting dipertahankan; rumah warga tidak dibongkar (Asistensi 4).
3. Ukuran eksisting: survei kelompok D3.2 & Andalalin 2023.
4. Skala 1:100 pada kertas A3.

STUDIO PERANCANGAN KOTA - KELOMPOK D3.2

Departemen Perencanaan Wilayah dan Kota

Dosen Pengampu: Novia Sari Ristianti, S.T., M.T.

SKALA	TANGGAL	LEMBAR
1 : 100 (A3)	28 Okt 2026	5 / 5