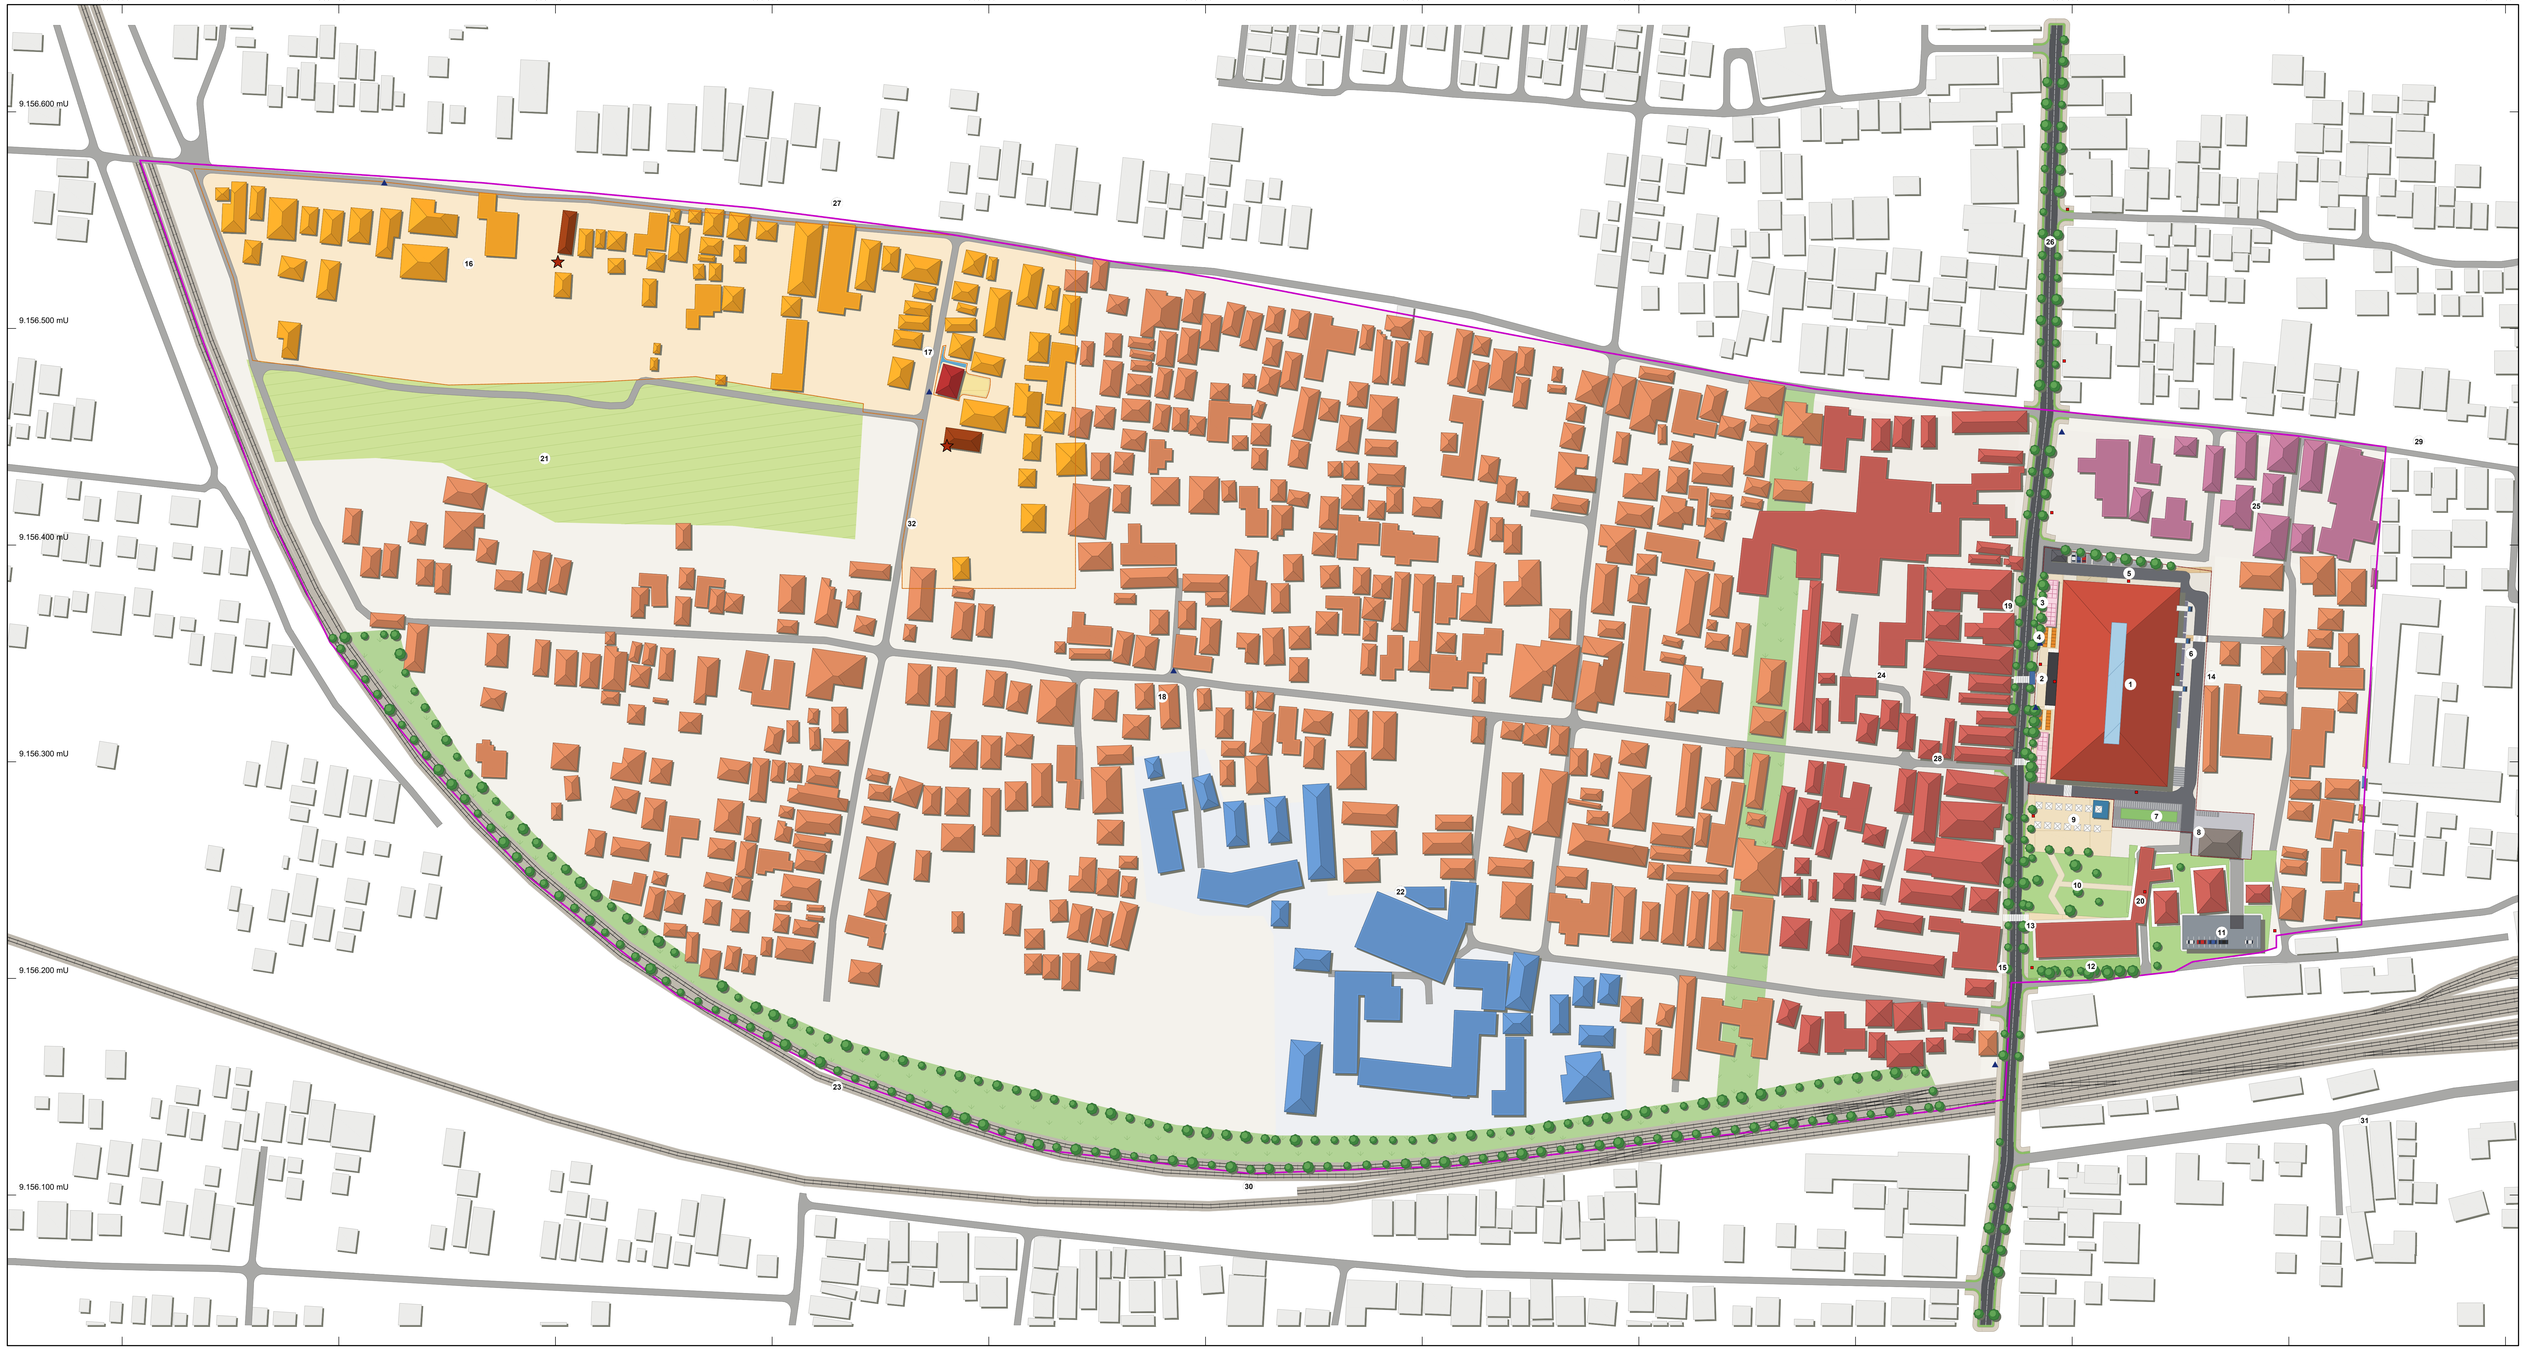


SITE PLAN

KAWASAN PASAR INDUK KROYA

"KROYA SMART UNIFIED MARKET"

KECAMATAN KROYA, KABUPATEN CILACAP, JAWA TENGAH

Revisi	: 23 Okt 2026 - rancangan pasar terbaru, PKL & showcase di halaman depan
Proyeksi	: Universal Transverse Mercator
Sistem Grid	: Grid UTM Zona 49 S
Datum Horizontal	: WGS 1984
Luas Delineasi	: 33,35 ha (Desa Kedawung & Desa Bajing)

STUDIO PERANCANGAN KOTA
KELOMPOK D3.2

Departemen Perencanaan Wilayah dan Kota
Dosen Pengampu: Novia Sari Ristianti, S.T., M.T.

SUMBER DATA

1. Delineasi tapak & zoning kelompok (GIS D3.2, 2026)
2. Bangunan eksisting: Building_Clip (BIG/OSM)
3. Jaringan jalan & rel: OpenStreetMap (Okt 2026); Jalan_Kecamatan
4. Rancangan Pasar Induk Kroya (site plan & denah lt 1-3)
5. Andalalin Pasar Kroya 2023 (antrean, bongkar-muat)
6. Titik produsen tempe: survei kelompok
7. Notulensi asistensi & analisis D3.2

ORIENTASI & SKALA

U

1 : 1.000


0 10 20 30 50 100 m

Kertas A0 (1189 x 841 mm)

Koordinat model = UTM 49S (meter).
Skala cetak 1:1.000;
1 mm kertas = 1 m lapangan.

INSET

Delineasi Rancang Kota dalam Kawasan Tapak NADI

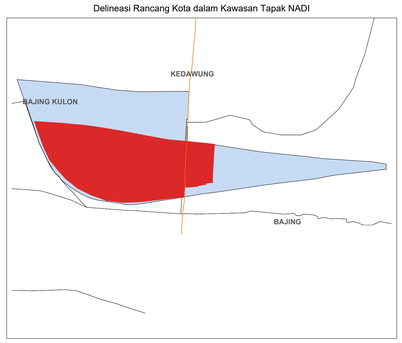

Kawasan Tapak NADI (72,70 ha)
Delineasi (33,35 ha)

LEGENDA

Batas, Jaringan & Konteks

- Batas delineasi (33,35 ha)
- Batas tapak pasar
- Jalan kolektor A. Yani + marka
- Jalan lingkar & servis pasar
- Jalan lokal/lingk. (fillet R 4 m)
- Trotoar 2 m
- Jalur hijau 1 m
- Rel kereta api
- Bangunan permukiman eksisting
- Bangunan perdagangan eksisting (Kato, ruko)
- Bangunan rumah-usaha eksisting
- Bangunan pendidikan eksisting
- Bangunan di luar delineasi
- Sawah / RTH

Kawasan Pasar

- Bangunan Pasar Induk (3 lt)
- Void / skylight pasar
- Halaman depan (plaza)
- Selasar & lapak PKL
- Lapak Showcase UMKM
- Plaza pasar & boulevard
- Gedung parkir UMKM/PKL 3 lt
- Parkir motor / mobil
- Petak bongkar-muat (SRP)
- Hard standing pemadam
- Halaman servis & utilitas
- Jalur pejalan kaki pedagang
- Zebra cross

Klaster UMKM & Simbol

- Klaster sentra tempe
- Rumah dalam klaster tempe
- Rumah produsen tempe (survei)
- Balai pelatihan UMKM
- Halaman jemur / display
- Biofilter limbah tempe
- Titik produsen tempe
- Pohon peneduh
- Hidran
- Penanda / papan petunjuk

KETERANGAN

1. Bangunan Pasar Induk 3 lt, 92 x 54 m
2. Pintu utama, lobi & kanopi
3. Lapak PKL (selasar beratap)
4. Showcase UMKM / pusat oleh-oleh
5. Jalan lingkar satu arah + parkir utara
6. Bongkar-muat 8 SRP
7. Parkir motor pengunjung
8. Halaman servis & utilitas
9. Plaza pasar (tenda kuliner sore)
10. Taman plaza
11. Gedung parkir UMKM/PKL 3 lt
12. Taman kawasan
13. Boulevard UMKM (ke stasiun)
14. Jalur pejalan kaki pedagang -> permukiman
15. RTH penyangga rel
16. Klaster sentra produksi tempe
17. Balai pelatihan UMKM + jemur + biofilter
18. Permukiman eksisting
19. Trotoar 2 m & jalur hijau A. Yani
20. Kato & ruko eksisting (terintegrasi pasar)
21. Sawah
22. Sarana pendidikan
23. RTH jalur hijau sempadan rel
24. Koridor perdagangan & jasa
25. Rumah tinggal komersial
26. Jl. Jend. A. Yani (kolektor primer)
27. Jl. Betet
28. Jl. Cendrawasih
29. Jl. Letkol Sudarso
30. Rel KA Prupuk/Maos - Kroya
31. Jl. Stasiun (ke Stasiun Kroya)
32. Jl. Ampas Waras

LUAS ELEMEN (diukur dari gambar)

Tapak pasar (rancangan): 9.694 m2
Plaza pasar: 1.045 m2
Gedung parkir (tapak): 558 m2
Klaster tempe: 38.446 m2
Lapak PKL / Showcase: 38 / 24 unit
Halaman depan PKL & showcase: 938 m2
Taman plaza & kawasan: 2.960 m2
Kato & ruko (eksisting): 1.522 m2
Balai pelatihan (lahan): 343 m2