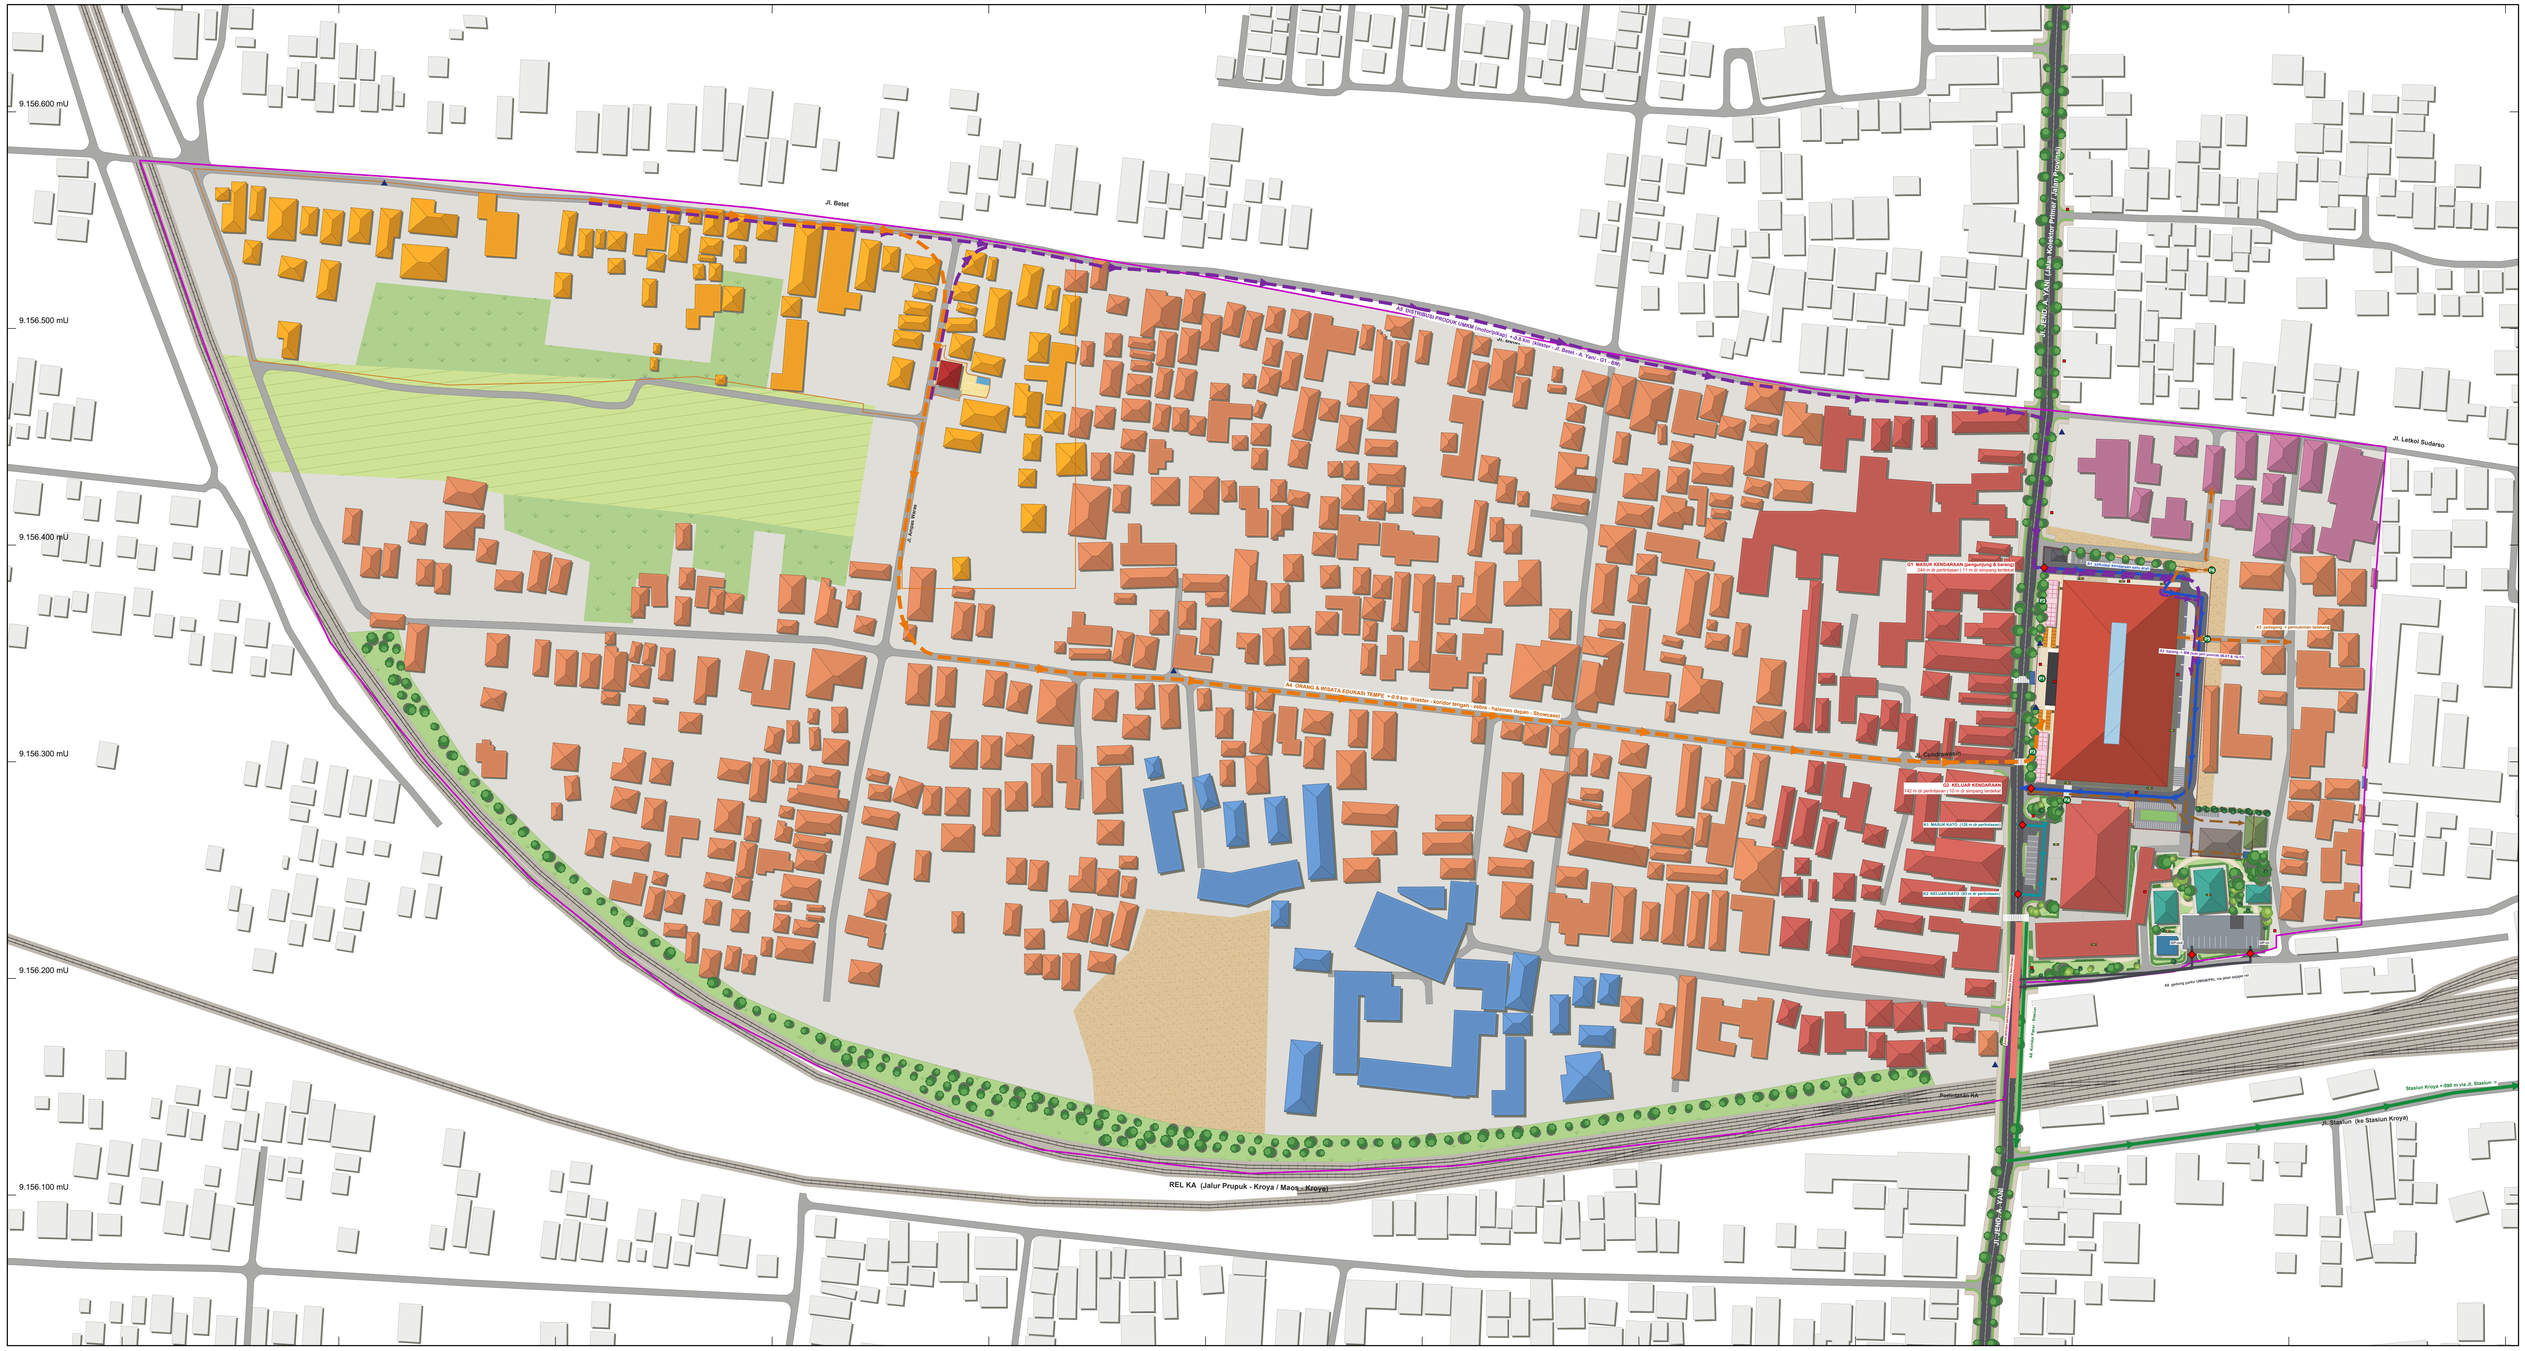



# PETA ALUR & SIRKULASI

## KAWASAN PASAR INDUK KROYA

## "KROYA SMART UNIFIED MARKET"

KECAMATAN KROYA, KABUPATEN CILACAP, JAWA TENGAH

| | |
|---|---|
| **Proyeksi** | : Universal Transverse Mercator |
| **Sistem Grid** | : Grid UTM Zona 49 S |
| **Datum Horizontal** | : WGS 1984 |
| **Luas Delineasi** | : 33,35 ha (Desa Kedawung & Desa Bajing) |


**STUDIO PERANCANGAN KOTA**
**KELOMPOK D3.2**

Departemen Perencanaan Wilayah dan Kota
Dosen Pengampu: Novia Sari Ristianti, S.T., M.T.


### SUMBER DATA

1. Delineasi tapak & zoning kelompok (GIS D3.2, 2026)
2. Bangunan eksisting: Building_Clip (BIG/OSM)
3. Jaringan jalan & rel: OpenStreetMap (Okt 2026); Jalan_Kecamatan
4. Rancangan Pasar Induk Kroya (site plan & denah lt 1-3)
5. Andalalin Pasar Kroya 2023 (masterplan, antrean, BM)
6. Penggunaan lahan hasil survei (Gunlah Tapak)
7. Notulensi asistensi & analisis D3.2

### ORIENTASI & SKALA

U

**1 : 1.000**


0 10 20 30 50 100 m

Kertas A0 (1189 x 841 mm)

Koordinat model = UTM 49S (meter).
Skala cetak 1:1.000;
1 mm kertas = 1 m lapangan.

### INSET

Delineasi Rancang Kota dalam Kawasan Tapak NADI

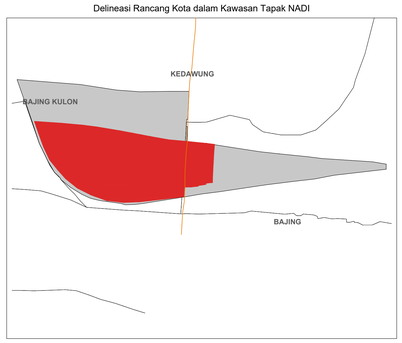


Kawasan Tapak NADI (72,70 ha)
Delineasi (33,35 ha)

### LEGENDA

**Batas, Jaringan & Konteks**
- Batas delineasi (33,35 ha)
- Batas tapak pasar
- Jalan kolektor A. Yani + marka
- Jalan lingkar pasar, Kato & GP
- Jalan lokal/lingk. (fillet R 4 m)
- Trotoar 2 m
- Jalur hijau 1 m
- Rel kereta api
- Bangunan permukiman eksisting
- Bangunan perdagangan eksisting (Kato, kios, ruko)
- Bangunan rumah-usaha eksisting
- Bangunan pendidikan eksisting
- Bangunan pelayanan umum (kantor pos)
- Bangunan di luar delineasi
- Latar: pekarangan / perkerasan eksisting
- Latar: tanah kosong eksisting
- Latar: kebun campuran eksisting
- Latar: sawah eksisting

**Kawasan Pasar**
- Bangunan Pasar Induk (3 lt)
- Void / skylight pasar
- Halaman depan (plaza)
- Selasar & lapak PKL
- Lapak Showcase UMKM
- Digital hub UMKM
- Halaman & parkir Kato (eksisting)
- Gedung parkir UMKM/PKL 3 lt
- Parkir motor / mobil
- Petak bongkar-muat (SRP)
- Hard standing pemadam
- Halaman servis & utilitas
- TPS3R: bangunan olah sampah
- Kontainer residu
- Jalur pejalan kaki pedagang / Kato
- Taman kawasan / RTH / taman saku
- RTH sempadan rel
- Semak / perdu
- Jalur & simpul taman

**Alur & Pergerakan**
- A1 Kendaraan pengunjung (satu arah)
- A2 Kendaraan barang ke BM
- A3 Pedagang ke permukiman belakang
- A4 Orang & wisata edukasi tempe
- A5 Distribusi produk UMKM
- A6 Koridor pejalan kaki stasiun
- A7 Kendaraan Kato (K1 -> K2)
- A8 Kendaraan gedung parkir (jl. sejajar rel)
- A9 Sampah terpilah -> TPS3R; residu -> TPA
- Zona antrean perlintasan 80 m
- Pintu kendaraan G, K, GP
- Pintu pejalan kaki P1-P6

### ALUR -> RESPON ANALISIS

| | |
|---|---|
| **A1** | Kendaraan pengunjung masuk G1 (barat laut), memutar satu arah, keluar G2 (barat daya) - Aksesibilitas; Andalalin |
| **A2** | Kendaraan barang lewat lajur utara ke 8 SRP timur, di luar jam puncak - Sirkulasi & parkir; Compatibility |
| **A3** | Pedagang ke permukiman belakang lewat gang eksisting (P5, P6) - Access; Asistensi |
| **A4** | Orang & wisata edukasi tempe +-0.9 km: koridor tengah - zebra - halaman depan - Showcase - Access; Pedestrian |
| **A5** | Distribusi produk UMKM +-0.8 km: Jl. Betet - A. Yani - G1 - BM, terpisah dari orang - Access; Compatibility |
| **A6** | Koridor pejalan kaki pasar - stasiun lewat trotoar A. Yani; tidak ada pintu kendaraan baru di zona antrean 80 m - Access; Andalalin |
| **A7** | Kato (Andalalin K, L, M) eksisting: masuk K1 - lajur satu arah 9 SRP - keluar K2 (fillet R 5 m), terpisah dari G2; pejalan kaki pasar - Kato lewat P4 - Compatibility |
| **A8** | Gedung parkir UMKM/PKL lewat jalan sejajar rel (GP-in timur, GP-out barat), tidak bercampur dengan sirkulasi pasar & bongkar-muat - Sirkulasi & parkir |
| **PKL** | PKL & showcase di halaman depan menghadap A. Yani: tetap dilewati arus pengunjung, tidak dipindah ke belakang - Aktivitas |
| **BM** | Bongkar-muat di sisi timur bangunan, permukiman dibatasi pagar & pohon - Compatibility; Kebisingan |
| **A9** | Zero waste: sampah dipilah di 16 titik pilah, gerobak lewat lajur timur ke TPS3R; organik -> maggot BSF & kompos, anorganik -> bank sampah, hanya residu ke TPA (truk keluar G2) |

**JARAK PINTU KENDARAAN (asistensi: >=100 m dari simpang, in & out berjarak)**

| Pintu | Fungsi | Perlintasan | Simpang Cendr. | Jl. sisi utara | Antar pintu |
|---|---|---|---|---|---|
| G1 | Masuk kendaraan | 244 m | 92 m | 11 m | 102 m |
| G2 | Keluar kendaraan | 142 m | 10 m | 113 m | 102 m |

G1/G2 mengikuti rancangan pasar (dipisah +-100 m, di luar zona antrean 80 m, fillet R 7 m). Kato: K1 masuk & K2 keluar sendiri (fillet R 5 m, di luar zona antrean). Gedung parkir: GP-in/GP-out dari jalan sejajar rel, terpisah dari pasar & BM.