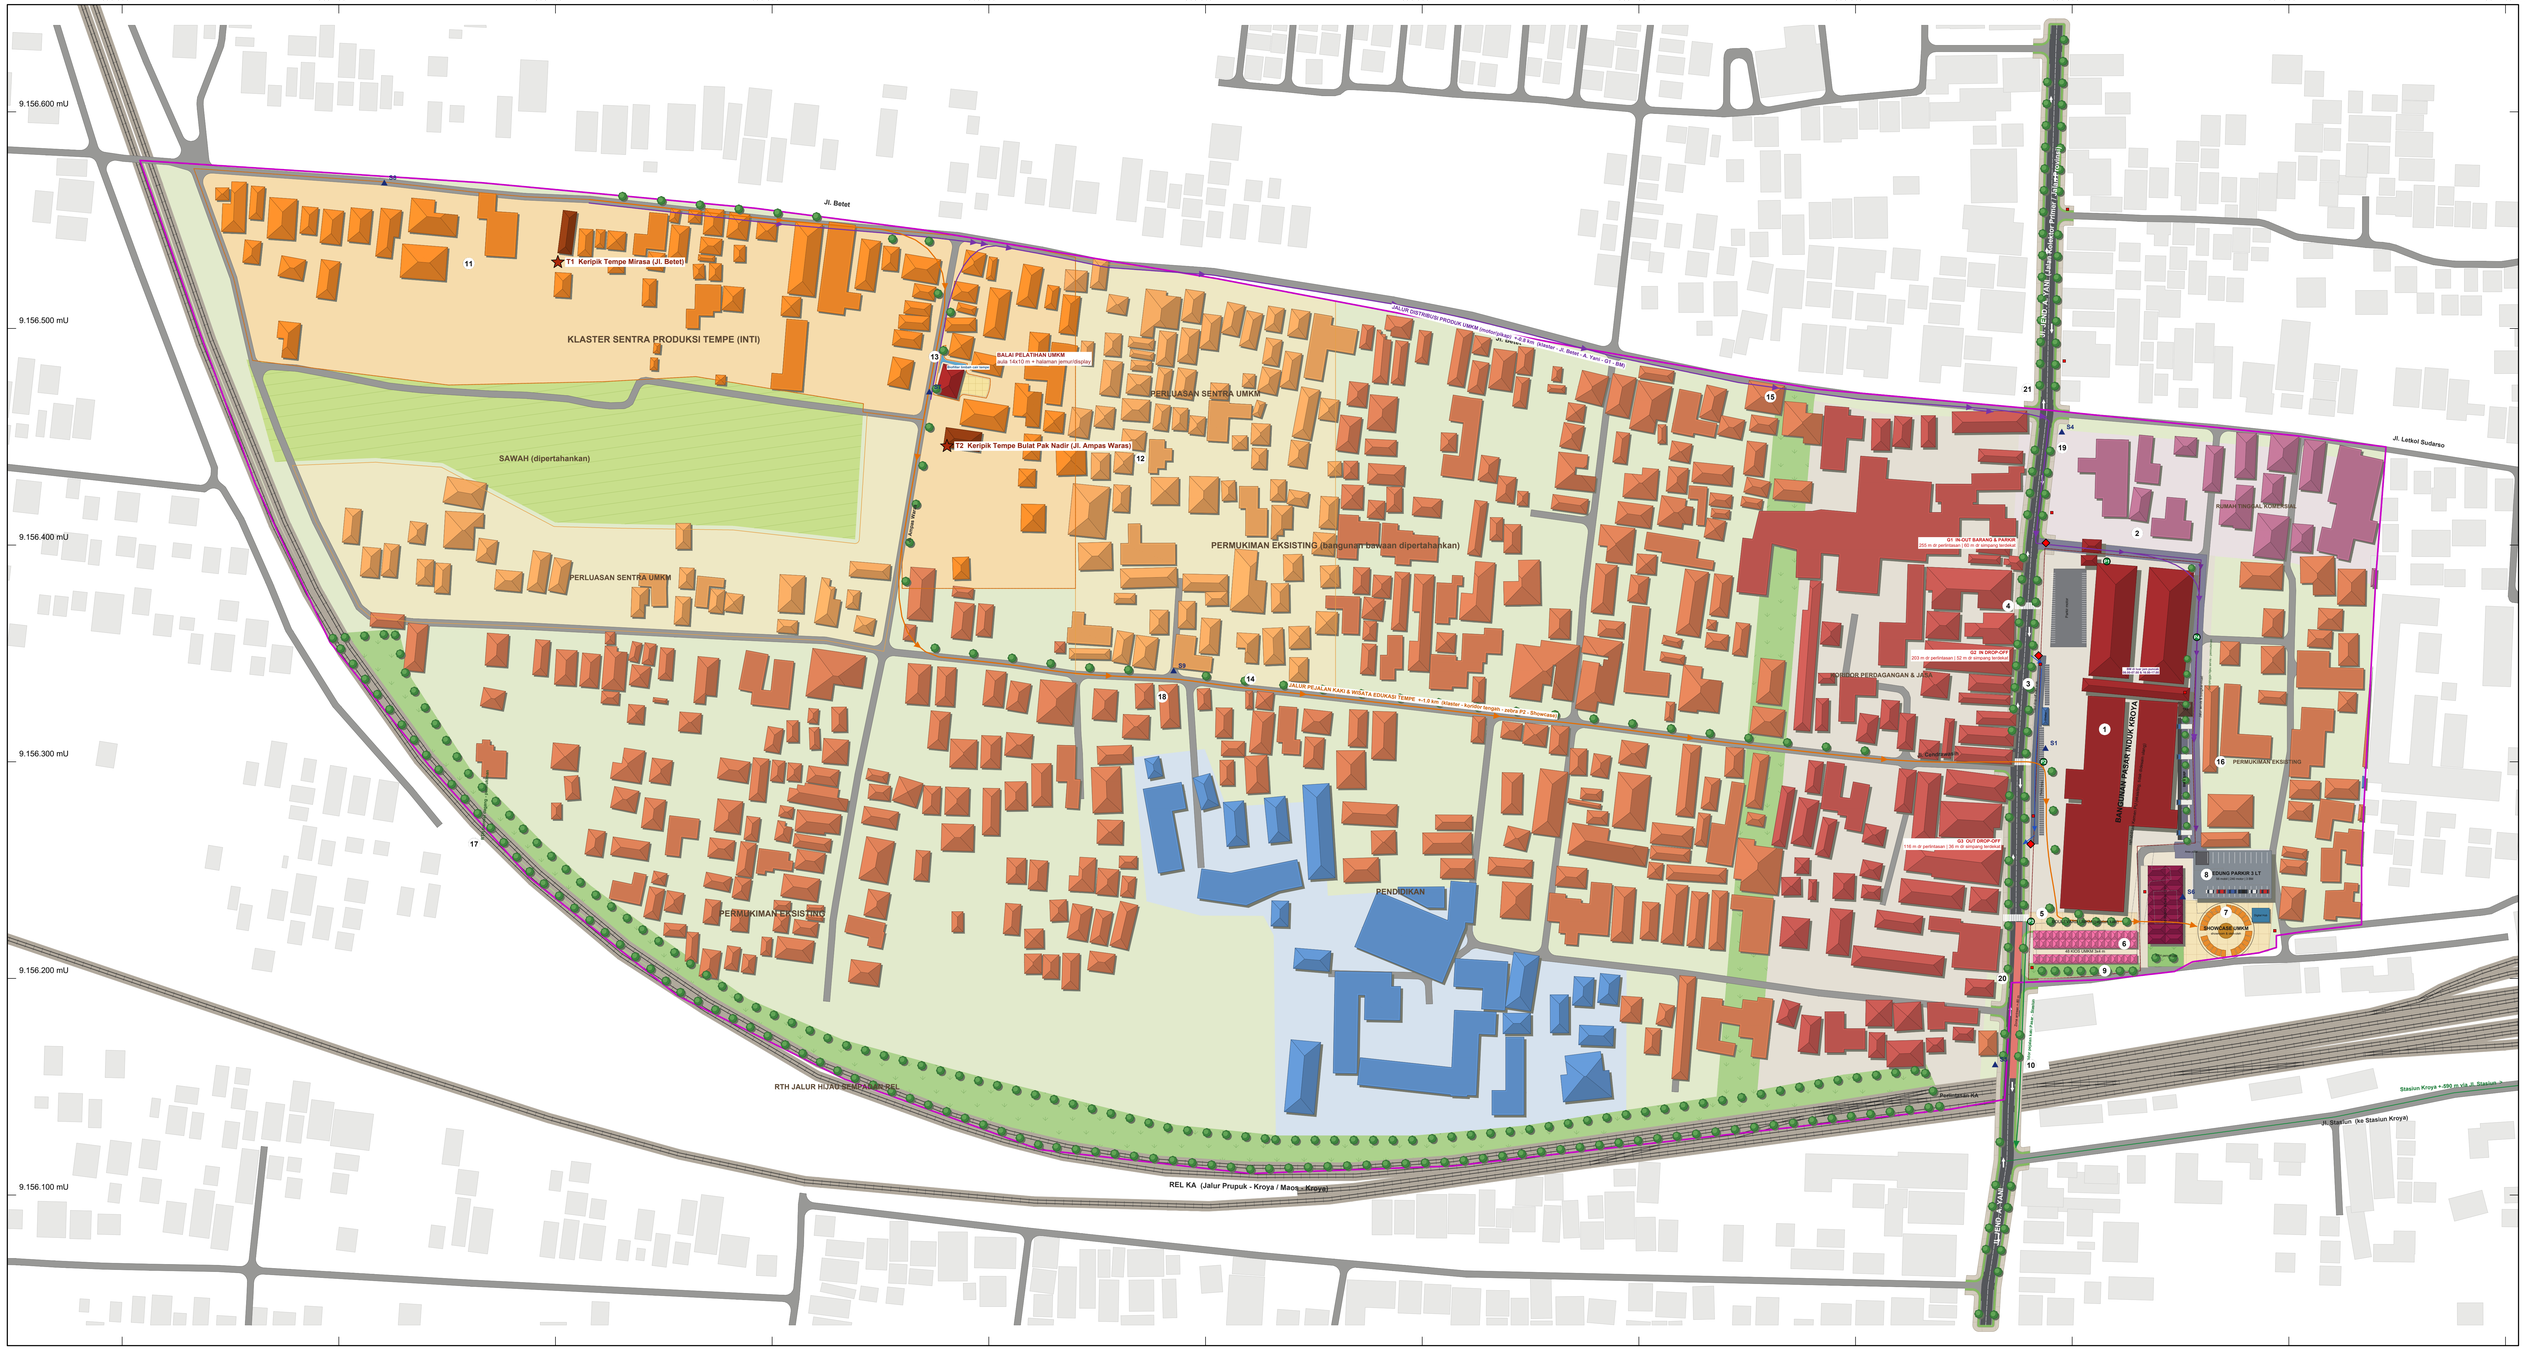


SITE PLAN

KAWASAN PASAR INDUK KROYA

"KROYA SMART UNIFIED MARKET"

KECAMATAN KROYA, KABUPATEN CILACAP, JAWA TENGAH

Revisi	: Asistensi 4 (1 Oktober 2026) - permukiman kembali ke kondisi eksisting
Proyeksi	: Universal Transverse Mercator
Sistem Grid	: Grid UTM Zona 49 S
Datum Horizontal	: WGS 1984
Luas Delineasi	: 33,35 ha (Desa Kedawung & Desa Bajing)

STUDIO PERANCANGAN KOTA KELOMPOK D3.2

Departemen Perencanaan Wilayah dan Kota

Dosen Pengampu: Novia Sari Ristianti, S.T., M.T.

SUMBER DATA

1. Delineasi tapak & zoning kelompok (GIS D3.2, 2026)
2. Bangunan eksisting: Building_Clip (BIG/OSM)
3. Jaringan jalan & rel: OpenStreetMap (unduh 7 Okt 2026); Jalan_Kecamatan
4. Bidang tanah (persil) Kawasan Tapak
5. Andalalin Pasar Kroya 2023 (HPL, antrean, bongkar-muat)
6. Titik produsen tempe: survei kelompok (Google Maps)
7. Notulensi Asistensi 4 & analisis D3.2

ORIENTASI & SKALA

U

1 : 1.000


0 10 20 30 50 100 m

Kertas A0 (1189 x 841 mm)

Koordinat model = UTM 49S (meter).
Skala cetak 1:1.000 pada layout ini;
1 mm kertas = 1 m lapangan.

INSET

Delineasi Rancang Kota dalam Kawasan Tapak NADI

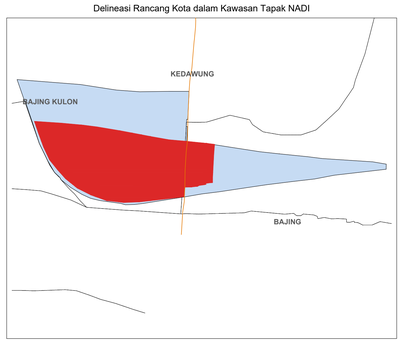

Kawasan Tapak NADI (72,70 ha)

Delineasi (33,35 ha)

LEGENDA

Batas, Jaringan & Zona

- Batas delineasi (33,35 ha)
- Batas HPL pasar (indikatif)
- Jalan kolektor (A. Yani) + marka
- Jalan lokal/lingk. (fillet R 4 m)
- Trotoar 2 m + jalur hijau 1 m
- Rel kereta api
- Zona permukiman
- Zona perdagangan & jasa
- Zona rumah tinggal komersial
- Zona pendidikan
- RTH / sempadan rel
- Sawah (dipertahankan)
- Bangunan di luar delineasi

Bangunan & Kawasan Pasar

- Bangunan permukiman (eksisting)
- Bangunan perdagangan (eksisting)
- Bangunan rumah-usaha (eksisting)
- Bangunan pendidikan (eksisting)
- Bangunan Pasar Induk (rehab Kemen PU)
- Kios UMKM 3x4 m
- Ruko 4,5x8 m, 2 lt
- Lapak Showcase UMKM
- Plaza Showcase / boulevard
- Gedung parkir 3 lt
- Jalur servis & bongkar-muat
- Petak bongkar-muat (SRP)
- Lajur drop-off satu arah
- Parkir motor
- Zona antrean perlintasan 80 m
- RTH penyangga

Klaster UMKM, Sirkulasi & Simbol

- Klaster sentra tempe (inti)
- Perluasan sentra UMKM
- Rumah dalam klaster inti
- Balai pelatihan UMKM
- Biofilter limbah tempe
- Titik produsen tempe (survei)
- Akses orang / wisata edukasi
- Akses barang (produk UMKM)
- Arus kendaraan penumpang
- Arus kendaraan barang
- Koridor pejalan kaki Pasar-Stasiun
- Pintu kendaraan G1-G3
- Pintu pejalan kaki P1-P4
- Zebra cross
- Pohon peneduh / penyangga
- Hidran
- Penanda / papan petunjuk S

RESPON ANALISIS -> ELEMEN SITE PLAN

1. Pasar Induk (eksisting, rehab Kemen PU) - Analisis aktivitas; Andalalin
2. G1 + jalur servis belakang pasar; 8 SRP bongkar-muat, TPS, area putar - Aksesibilitas; Sirkulasi & parkir
3. G2-G3 lajur drop-off satu arah, shelter bajaj/becak motor, parkir motor - Sirkulasi & parkir
4. 3 zebra cross + trotoar 2 m & jalur hijau A. Yani - Pedestrian; Kebisingan; Livability
5. Boulevard UMKM: jalan servis di zona antrean ditutup bagi kendaraan - Access; Andalalin
6. Blok kios: 48 kios UMKM + 16 ruko (relokasi PKL bahu jalan) - Pendukung aktivitas
7. Showcase UMKM = showroom & pusat oleh-oleh (24 lapak, panggung demo, digital hub) - Asistensi; Identity
8. Gedung parkir 3 lt (56 mobil, 240 motor, 3 BM kios) - Kebutuhan ruang; Parkir
9. RTH penyangga & jalur hijau sempadan rel - Kebisingan; Ruang terbuka; Drainase
10. Koridor pejalan kaki Pasar-Stasiun, tanpa akses kendaraan di zona antrean - Access; Asistensi
11. Klaster sentra tempe inti: produksi tetap di rumah (2 produsen survei) - Asistensi; Activity
12. Perluasan sentra UMKM: tempe & olahan lain (sale/keripik pisang, jamu) - Asistensi
13. Balai pelatihan UMKM + halaman jemur/display + biofilter limbah cair tempe - Asistensi; Sanitasi
14. Akses ORANG klaster-pasar: koridor tengah, zebra P2, peneduh bap +-18 m (+-1.0 km) - Access; Pedestrian
15. Akses BARANG klaster-pasar: Jl. Betet - A. Yani - G1 - BM (+-0.8 km), terpisah dari orang - Access; Compatibility
16. Penyangga hijau servis-permukiman; BM di luar jam puncak - Compatibility; Kebisingan
17. RTH transisi koridor dagang - permukiman dipertahankan - Compatibility
18. Permukiman: bangunan bawaan dipertahankan, tidak ditata ulang - Asistensi
19. Penanda S1-S9 & hidran kondor komersial (50-90 m) - Penanda; Pemadam kebakaran
20. Zona antrean perlintasan 80 m: tanpa pintu kendaraan baru - Andalalin
21. Tikungan & simpang jalan di-fillet R 4 m + marka lajur A. Yani - Aksesibilitas

JARAK PINTU KENDARAAN (asistensi: >=100 m dari simpang, >=50 m antar pintu)

Pintu	Fungsi	Perlintasan	Simpang Cendr.	Simpang Betet	Antar pintu
G1	In-out barang & parkir	255 m	104 m	60 m	G2: 52 m
G2	In drop-off penumpang	203 m	52 m	112 m	G3: 87 m
G3	Out drop-off penumpang	116 m	36 m	199 m	G1: 139 m

Di Jl. A. Yani sisi pasar simpang berjarak 52-104 m, sehingga 100 m tidak dapat dipenuhi; pintu ditempatkan di titik terjauh dari simpang dan di luar zona antrean 80 m (Andalalin).

LUAS ELEMEN (diukur dari gambar) vs TABEL KEBUTUHAN RUANG

HPL Pasar Induk (indikatif): 12.656 m2 [tabel: 13.978 (Andalalin)]
Blok kios + ruko (tapak): 1.787 m2 [tabel: 3.113 (incl. lorong & boulevard)]
RTH penyangga: 446 m2 [tabel: 1.117]
Perluasan sentra UMKM: 38.201 m2 [tabel: -]
Showcase UMKM: 1.063 m2 [tabel: 1.320]
Gedung parkir (tapak): 799 m2 [tabel: 864]
Klaster tempe inti: 38.446 m2 [tabel: -]
Balai pelatihan (lahan): 343 m2 [tabel: -]