D3.2

PERUMUSAN DELINEASI, POTENSI MASALAH, DAN KONSEP PERENCANAAN KAWASAN

KECAMATAN KROYA, KABUPATEN CILACAP

Dosen Pengampu:
Novia Sari Ristianti, S.T., M.T.

ANGGOTA KELOMPOK

21040124130062
Ariyanto Rafi Nugroho

21040124140126
Erlinda Alifia Dhiya S.

21040124120036
Calvin Chi Wai Harmita

21040124120016
Ernest Nove Trinita S.

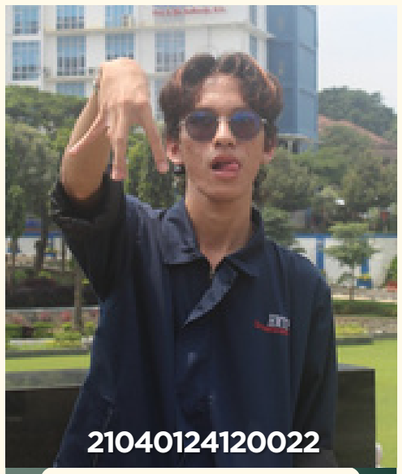

21040124120022
Ezekiel Christian S.

21040124140163
Kanaya Aprilia Putri

21040124190124
Widyatmaja Aryasatya P.

21040124190193
Zhillan Qisa Zhahiran

Delineasi Kawasan

Desa Kedawung & Desa Bajing

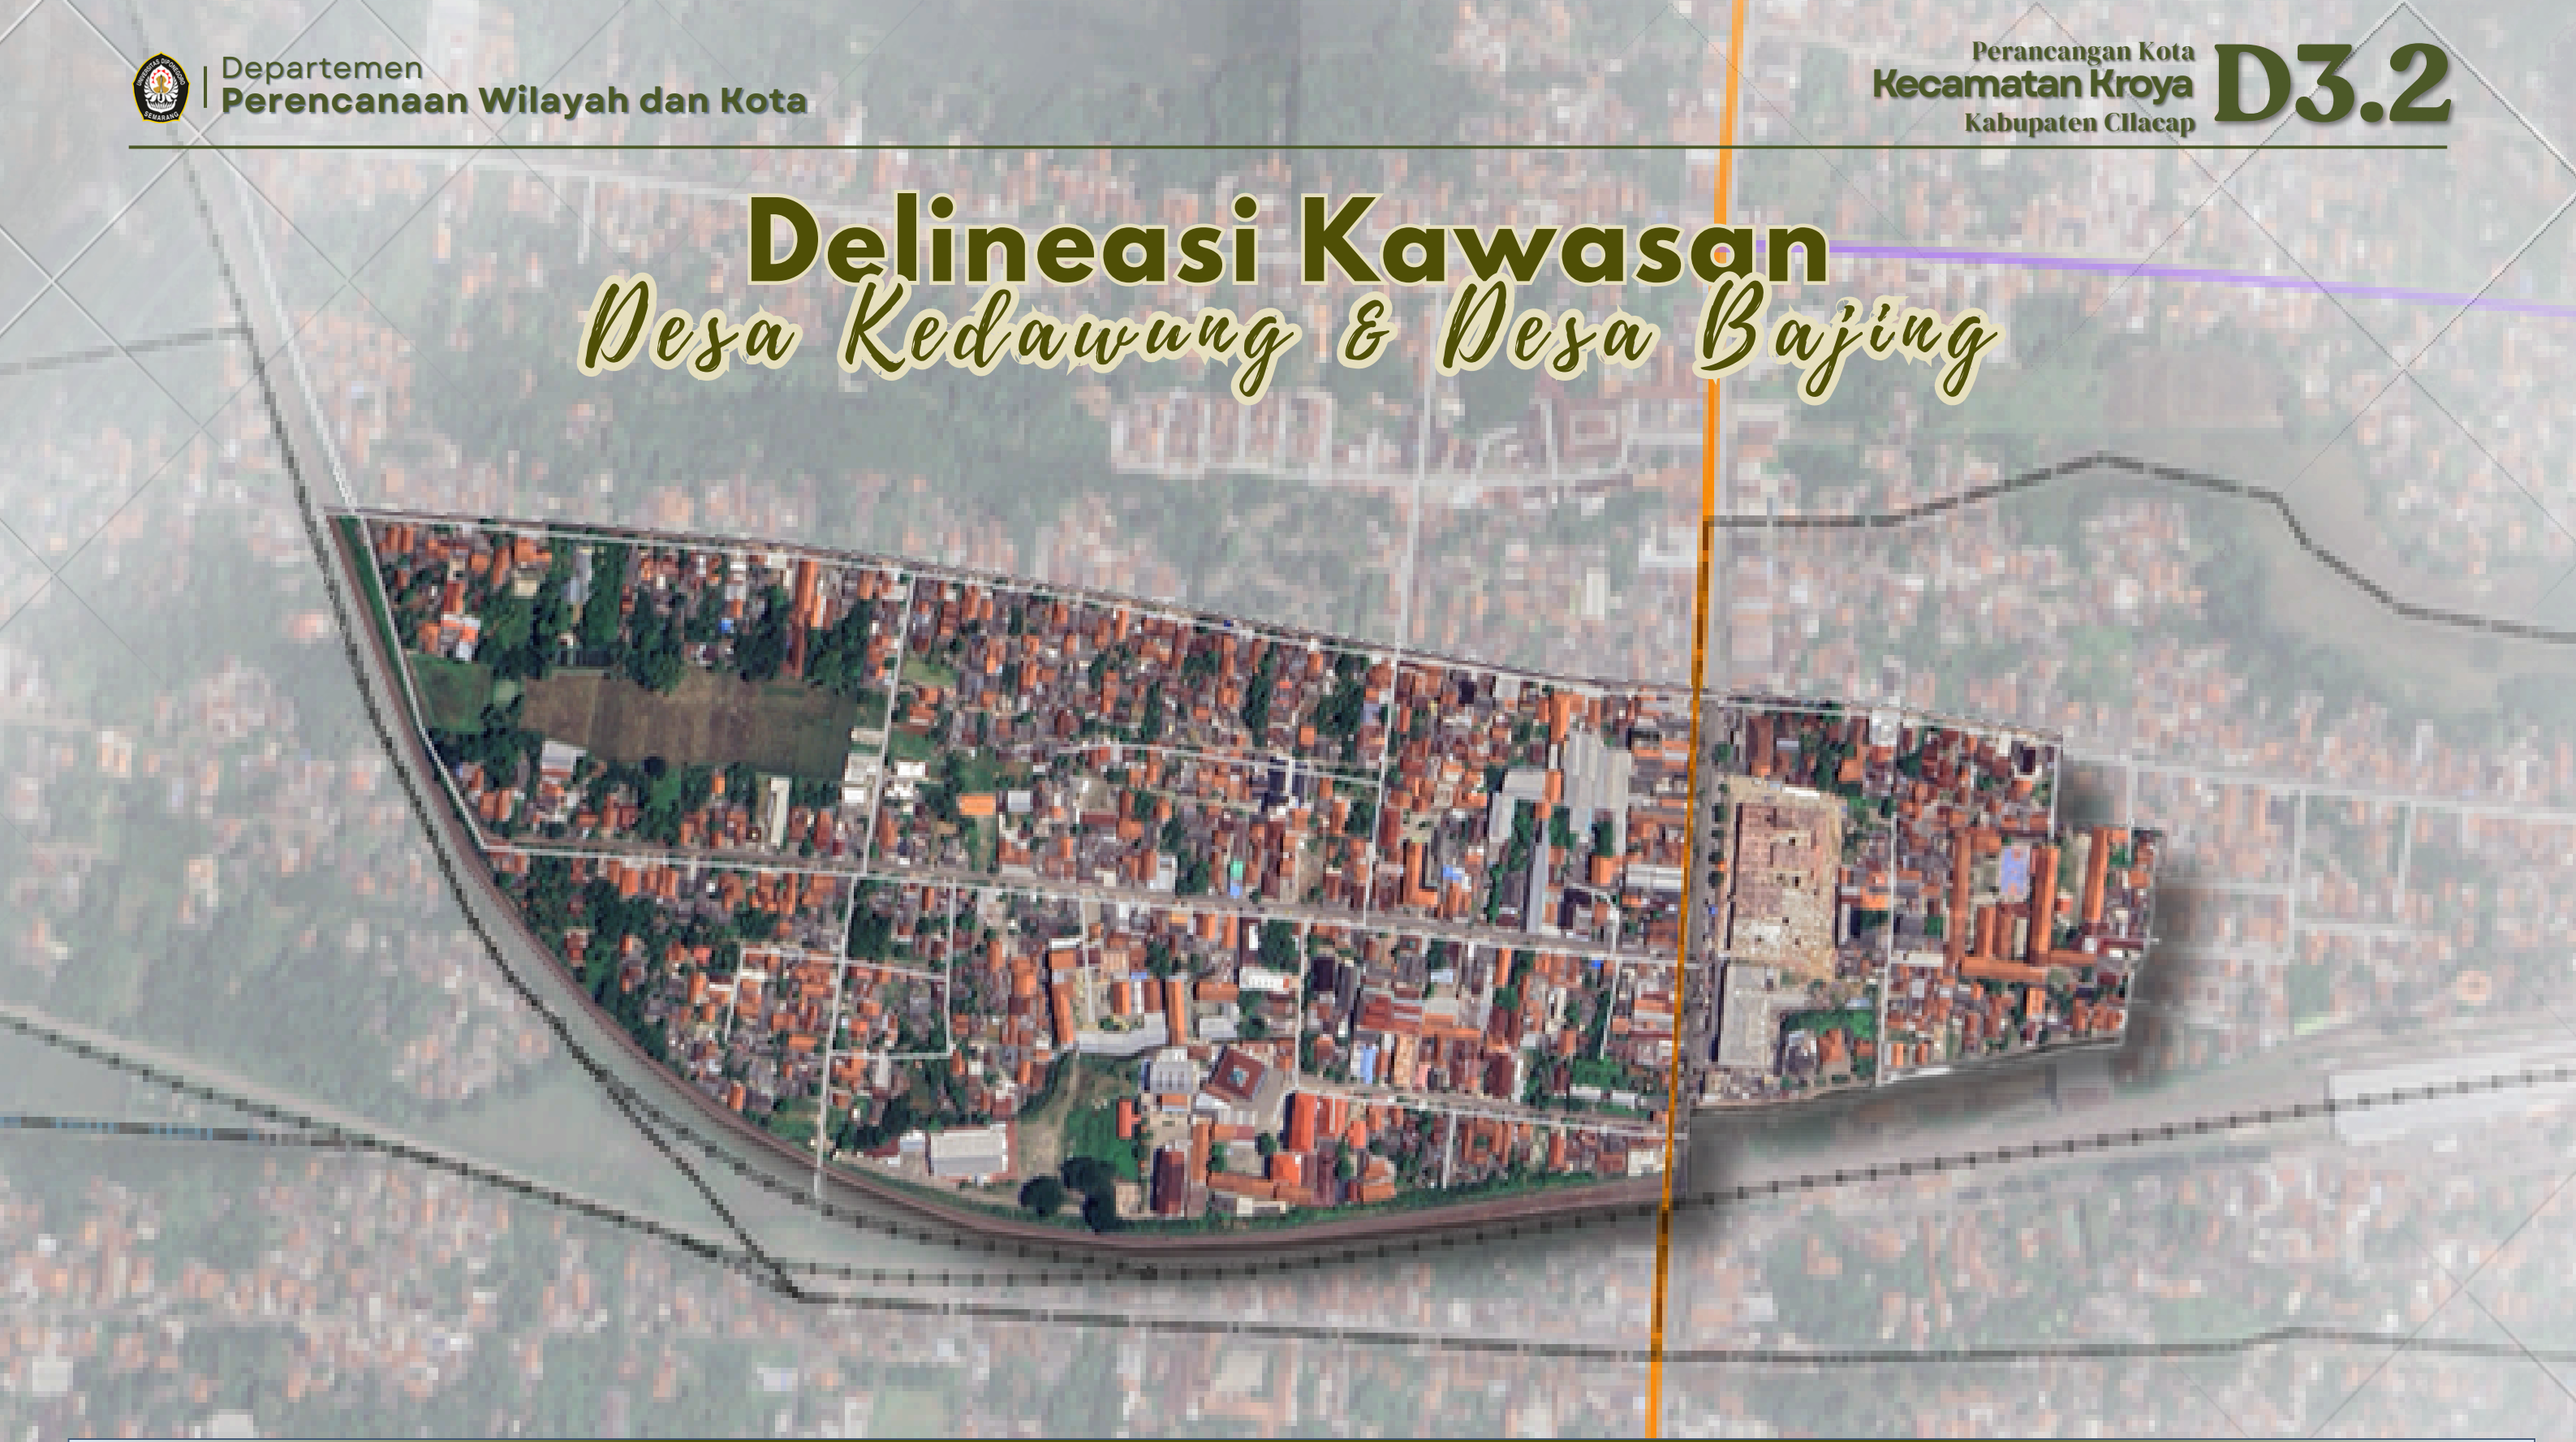

Keterangan

Lokasi tapak di Kawasan Perkotaan Kroya memiliki **luas 35,49 ha**. Struktur ruang yang dipengaruhi oleh keberadaan koridor **jalan kolektor (Jalan Jendral A.Yani)** serta **jalur rel kereta api** yang melintas di kawasan. Permukiman cenderung berkembang linear mengikuti koridor transportasi, dengan kepadatan bangunan yang lebih tinggi di sepanjang akses utama.

Analisis Potensi dan Masalah

P1

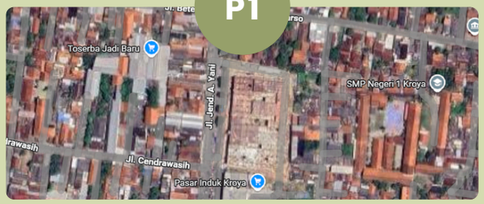

Mixed-use yang sudah terbentuk secara alami
Keberadaan pasar, sekolah, dan permukiman dalam satu kawasan menciptakan keragaman aktivitas yang dapat menjadi dasar pembentukan kawasan dengan keragaman fungsi dan interaksi masyarakat yang kuat

P2

Keberadaan **Pasar Induk Kroya sebagai pasar induk skala kabupaten dengan 1.616 pedagang** (248 kios, 1.148 los, dan 220 lemprakan). Tingginya aktivitas perdagangan menjadikannya **pusat distribusi barang bagi wilayah Kroya dan sekitarnya.**

P3

Konektivitas yang tinggi didukung oleh **jalan kolektor primer yang terhubung dengan jalan nasional** (Jalan Nasional Rte 3). Jalan ini menghubungkan **pusat kegiatan di Kroya dengan desa-desa di sekitarnya** sehingga memudahkan perpindahan barang dan manusia.

Keterangan
- Potensi
- Masalah

M1

Kemacetan lalu lintas terjadi di sepanjang Jalan Jenderal Ahmad Yani, di sekitar perlintasan kereta api dan kawasan pasar. Sebanyak **147 perjalanan kereta api yang melintasi perlintasan** setiap hari menyebabkan antrean kendaraan dan menghambat mobilitas.

M2

Mangkraknya revitalisasi Pasar Induk Kroya menyebabkan pedagang harus berjualan di lokasi sementara dengan fasilitas terbatas dan kapasitas yang tidak memadai, sehingga **aktivitas perdagangan kurang optimal dan pendapatan pedagang menurun.**

M3

Kebutuhan fasilitas pejalan kaki *dan pesepeda,* belum terpenuhi di sepanjang Jalan Jenderal Ahmad Yani menyebabkan ruang pergerakan terbatas. Kondisi ini **mengurangi kenyamanan** serta **meningkatkan potensi risiko keselamatan pengguna jalan *non-motorized.***

Perumusan Isu Lokasi Perancangan Kota

Menurunnya efisiensi distribusi barang dan daya saing ekonomi Kroya sebagai pusat distribusi regional, serta menurunnya kualitas dan keselamatan ruang publik bagi masyarakat sekitar.

Belum optimalnya integrasi antara pasar induk kroya dengan sistem transportasi dan ruang pergerakan kawasan

Keragaman aktivitas kawasan berbenturan dengan gangguan mobilitas akibat perlintasan kereta api

Potensi

Keberadaan pasar, sekolah, dan permukiman menciptakan keragaman fungsi dan interaksi masyarakat yang kuat.

Masalah

Kemacetan lalu lintas terjadi di sepanjang Jalan Ahmad Yani yang dilintasi oleh rel kereta api, mengakibatkan banyaknya frekuensi perjalanan kereta api.

Aktivitas perdagangan yang tinggi di Pasar Induk Kroya, namun tidak diiringi dengan keseimbangan penataan ruang perdagangan yang optimal.

Potensi

Keberadaan Pasar Induk Kroya (skala kabupaten) menjadikan Kawasan Kroya sebagai pusat perdagangan dan distribusi barang.

Masalah

Mangkraknya revitalisasi Pasar Induk Kroya membuat para pedagang terpaksa berjualan di tempat lain, sehingga pendapatan para pedagang menurun.

Jaringan jalan yang saling terhubung belum didukung dengan jalur pejalan kaki dan pesepeda.

Potensi

Kawasan dengan konektivitas yang tinggi didukung oleh jalan kolektor yang terhubung dengan jalan nasional, sehingga memudahkan mobilisasi barang dan orang.

Masalah

Kebutuhan akan fasilitas jalur pejalan kaki dan pesepeda yang belum terpenuhi, pada area sepanjang koridor utama Jalan Ahmad Yani menyebabkan kurangnya kenyamanan dalam beraktivitas serta meningkatkan risiko akan keselamatan pengguna jalan.

ISU ANTARA | **ISU UTAMA** | **DAMPAK**

Konsep Dasar *Transit-Linked Market*

KONSEP

Pasar Induk Kroya sebagai Simpul Multimoda (*Transit-Linked Market*)

Tujuan Utama

Mewujudkan Pasar Induk Kroya sebagai simpul transportasi dan aktivitas ekonomi-sosial yang terintegrasi, untuk meningkatkan efisiensi distribusi, mengurangi kemacetan, dan menciptakan ruang gerak yang aman bagi semua pengguna.

Isu Utama

Belum optimalnya integrasi Pasar Induk Kroya dengan sistem transportasi dan ruang pergerakan kawasan.

Potensi

Keberadaan pasar, sekolah, dan permukiman menciptakan keragaman fungsi dan interaksi masyarakat yang kuat.

Potensi

Keberadaan Pasar Induk Kroya (skala kabupaten) menjadikan Kawasan Kroya sebagai pusat perdagangan dan distribusi barang.

Potensi

Kawasan dengan konektivitas yang tinggi didukung oleh jalan kolektor yang terhubung dengan jalan nasional, sehingga memudahkan mobilisasi barang dan orang.

Masalah

Kemacetan lalu lintas terjadi di sepanjang Jalan Ahmad Yani yang dilintasi oleh rel kereta api, mengakibatkan banyaknya frekuensi perjalanan kereta api.

Masalah

Mangkraknya revitalisasi Pasar Induk Kroya membuat para pedagang terpaksa berjualan di tempat lain, sehingga pendapatan para pedagang menurun.

Masalah

Kebutuhan akan fasilitas jalur pejalan kaki dan pesepeda yang belum terpenuhi, pada area sepanjang koridor utama Jalan Ahmad Yani menyebabkan kurangnya kenyamanan dalam beraktivitas serta meningkatkan risiko akan keselamatan pengguna jalan.

Konsep Dasar dan Justifikasi *Transit-Linked Market*

KONDISI EKSISTING

Aktivitas dan Mobilitas

Keberadaan pasar, sekolah, dan permukiman menciptakan keragaman fungsi dan interaksi masyarakat yang kuat

Kemacetan lalu lintas terjadi di sepanjang Jalan Ahmad Yani yang dilintasi oleh rel kereta api, mengakibatkan banyaknya frekuensi perjalanan kereta api.

Perdagangan Pasar Induk

Keberadaan Pasar Induk Kroya (skala kabupaten) menjadikan Kawasan Kroya sebagai pusat perdagangan dan distribusi barang

Mangkraknya revitalisasi Pasar Induk Kroya membuat para pedagang terpaksa berjualan di tempat lain, sehingga pendapatan para pedagang menurun.

Sirkulasi dan Jalur Pejalan Kaki

Kawasan dengan konektivitas yang tinggi didukung oleh jalan kolektor yang terhubung dengan jalan nasional, sehingga memudahkan mobilisasi barang dan orang.

Kebutuhan akan fasilitas jalur pejalan kaki dan pesepeda yang belum terpenuhi, pada area sepanjang koridor utama Jalan Ahmad Yani menyebabkan kurangnya kenyamanan dalam beraktivitas serta meningkatkan risiko akan keselamatan pengguna jalan.

Konsep

Transit-Linked Market merupakan konsep pengembangan kawasan pasar induk yang berorientasi pada sistem **transportasi publik**, sebagai penerapan pendekatan **Transit Oriented Development (TOD)** yang difokuskan pada integrasi aktivitas perdagangan pasar induk. Konsep ini bertujuan menjadikan **Pasar Induk Kroya** sebagai simpul multimoda yang memadukan fungsi **transportasi dan aktivitas ekonomi-sosial secara terintegrasi**, guna meningkatkan efisiensi distribusi barang, mengurangi kemacetan akibat perlintasan kereta api, serta menciptakan ruang gerak yang aman dan nyaman bagi seluruh pengguna, termasuk pejalan kaki dan pesepeda.

Potensi

Masalah

IMPLEMENTASI

Penataan ulang jalur sirkulasi dan pengaturan jadwal pergerakan di perlintasan kereta api Jalan Ahmad Yani untuk mengurangi konflik dan kemacetan lalu lintas.

Revitalisasi Pasar Induk Kroya dan penataan ruang dagang untuk mendukung aktivitas ekonomi serta integrasinya dengan simpul transportasi (stasiun).

Penyediaan dan penataan jalur pejalan kaki serta pesepeda di sepanjang koridor utama Jalan Ahmad Yani guna meningkatkan kenyamanan dan keselamatan pengguna jalan.

Best Practice

Pasar Tanah Abang, Jakarta

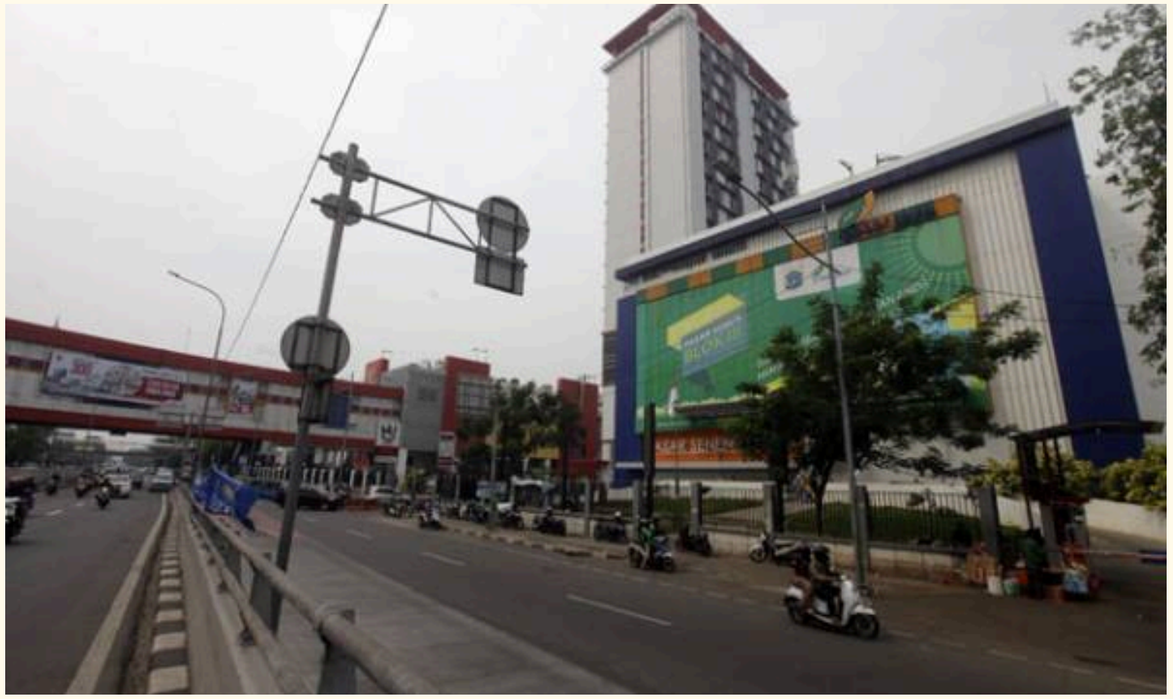

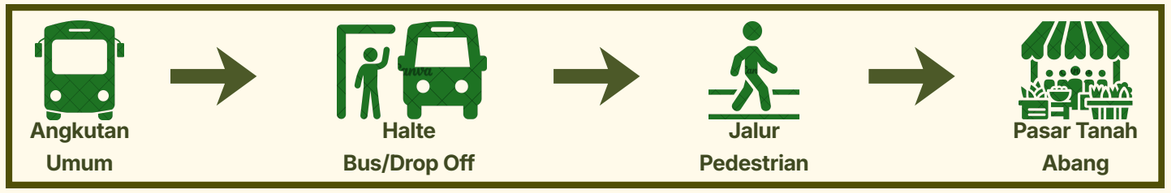

KETERANGAN

- Pasar menjadi pusat tujuan perjalanan, sedangkan angkutan umum berfungsi membawa pengguna dari berbagai bagian kota menuju kawasan pasar.
- Halte dan titik pemberhentian angkutan umum ditempatkan/diatur agar memiliki hubungan yang mudah dengan area perdagangan.
- Arus penumpang diarahkan melewati kawasan perdagangan, sehingga perjalanan dari halte menuju tujuan sekaligus menghasilkan foot traffic bagi pedagang.
- Aktivitas perdagangan dan transportasi dipisahkan secara fungsional, sehingga kendaraan umum tidak harus masuk ke area pedestrian tetapi tetap memberikan akses yang dekat.

HAL YANG DAPAT DIADAPTASI

- Menempatkan halte/titik transit dekat dengan pusat perdagangan.
- Membentuk koridor pedestrian komersial dari titik transit menuju pasar.
- Mengarahkan UMKM dan perdagangan lokal pada koridor yang memiliki arus pejalan kaki tinggi

Best Practice

Chatuchak Market, Bangkok

KETERANGAN

- Pasar menjadi destination utama, sementara jaringan angkutan umum menyediakan akses dari berbagai arah.
- Terdapat beberapa titik akses menuju kawasan pasar sehingga pengguna tidak terkonsentrasi pada satu pintu.
- Titik turun angkutan umum diarahkan ke akses pedestrian menuju pasar.
- Setelah turun, pengguna bergerak melalui jalur pedestrian yang terhubung dengan zona-zona perdagangan.
- Aktivitas perdagangan dibuat berkelompok/zoning, sehingga pengguna dapat bergerak dari satu zona ke zona lain.

HAL YANG DAPAT DIADAPTASI

- Menghubungkan beberapa rute angkutan umum dengan kawasan perdagangan.
- Menyediakan lebih dari satu akses pedestrian untuk menghindari penumpukan pada satu titik.
- Mengelompokkan perdagangan, UMKM, dan komoditas lokal dalam zona yang saling terhubung.

Bab I

ANALISIS NON-FISIK (ANALISIS AKTIVITAS)

Karakteristik Aktivitas Kawasan

PERDAGANGAN

- Aktivitas perdagangan **memiliki intensitas yang tinggi dengan keberadaan Pasar Induk Kroya** sebagai pusat perdagangan dan distribusi barang.
- Pasar Induk Kroya memiliki skala pelayanan kabupaten dengan 1.616 pedagang yang terdiri atas kios, los, dan lemprakan.
- Aktivitas perdagangan **terkonsentrasi di sekitar Pasar Induk Kroya dan koridor Jalan Jenderal Ahmad Yani**.
- Aktivitas perdagangan tidak hanya melayani masyarakat sekitar, tetapi juga mendukung distribusi barang ke wilayah Kroya dan sekitarnya.

TRANSPORTASI

- Aktivitas transportasi memiliki **intensitas yang tinggi** karena didukung jalan kolektor primer yang terhubung dengan jaringan jalan nasional.
- Pergerakan kawasan meliputi mobilitas manusia dan barang menuju pusat kegiatan di Kroya maupun desa-desa di sekitarnya.
- Jalur kereta api yang melintas di kawasan turut menjadi bagian dari sistem pergerakan kawasan.
- Aktivitas kendaraan berkonflik dengan perlintasan kereta api, terutama di Jalan Jenderal Ahmad Yani, sehingga menimbulkan antrean dan kemacetan.

HUNIAN

- Hunian berkembang secara **linear** mengikuti koridor transportasi, terutama pada jaringan jalan utama kawasan.
- Kepadatan bangunan hunian cenderung **lebih tinggi di sepanjang akses utama**.
- Hunian berada berdampingan dengan berbagai fungsi kawasan, terutama perdagangan dan fasilitas pendidikan, sehingga membentuk keragaman aktivitas.
- Beberapa hunian juga memiliki fungsi ekonomi, seperti warung makan, usaha rumahan, dan kost.

DISTRIBUSI

- Aktivitas distribusi barang berpusat pada Pasar Induk Kroya sebagai pusat distribusi berskala kabupaten.
- Distribusi barang melibatkan pergerakan keluar-masuk barang melalui jaringan jalan utama kawasan.
- Aktivitas distribusi didukung oleh konektivitas jalan kolektor primer yang terhubung dengan jalan nasional.
- Tingginya aktivitas distribusi belum sepenuhnya didukung oleh integrasi pasar dengan sistem transportasi, sehingga efisiensi distribusi masih belum optimal.

Jenis Aktivitas dan Fungsi Ruang

Kelompok Aktivitas	Jenis Aktivitas	Jenis Bangunan/ Ruang	Fungsi Ruang	Karakteristik Ruang	Penggunaan Ruang
Perdagangan	Kegiatan komersial intensitas tinggi	Pasar induk & ruko sepanjang koridor	Menyediakan ruang jual-beli dan distribusi barang skala kabupaten, terpusat di Pasar Induk Kroya	Terkonsentrasi di Pasar Induk Kroya dan koridor Jl. Jenderal Ahmad Yani; 1.616 pedagang (kios, los, lemprakan)	Pedagang & masyarakat sekitar, serta pelaku distribusi barang ke wilayah Kroya dan sekitarnya
Transportasi	Pergerakan manusia dan barang	Jaringan jalan kolektor primer & jalur rel KA	Menghubungkan kawasan dengan jaringan jalan nasional serta memfasilitasi mobilitas menuju pusat kegiatan	Intensitas tinggi; berpotongan dengan jalur KA di Jl. Jenderal Ahmad Yani sehingga rawan antrean/kemacetan	Pengguna kendaraan pribadi, angkutan barang, dan penumpang KA
Hunian	Bertempat tinggal, sebagian bercampur usaha	Rumah tunggal & rumah-toko (mixed-use kecil)	Tempat tinggal penduduk yang berdampingan dengan fungsi ekonomi (warung, usaha rumahan, kost)	Berkembang linear mengikuti koridor jalan utama; kepadatan lebih tinggi di sepanjang akses utama	Penduduk setempat, sebagian merangkap pelaku usaha kecil (warung, kost)
Distribusi	Koleksi & distribusi barang	Pasar induk sebagai simpul logistik	Pusat pengumpulan dan penyaluran barang berskala kabupaten	Bergantung pada jaringan jalan kolektor primer; integrasi dengan sistem transportasi belum optimal	Pelaku usaha distribusi/logistik yang melayani keluar-masuk barang ke/dari kawasan

Pengguna Kawasan

Analisis pengguna dilakukan untuk mengidentifikasi jumlah individu pada setiap kelompok aktivitas di kawasan perencanaan. Melalui analisis ini, kebutuhan ruang dapat ditentukan secara lebih tepat sesuai dengan jumlah pengguna yang ada. Perhitungan dilakukan dengan **menghitung jumlah unit rumah** yang terdapat pada kawasan. Estimasi jumlah pengguna yang tinggal di kawasan tersebut diperoleh melalui perhitungan menggunakan rumus berikut:

Jumlah pengguna kawasan = Jumlah rumah di kawasan x Standar Jiwa per Rumah berdasarkan SNI

**Dalam laporan ini digunakan standar 4 jiwa per rumah*

Sehingga diperoleh

Jumlah pengguna kawasan = 587 x 4 = 2.348 Jiwa

Terdapat fasilitas-fasilitas yang tersedia di dalam kawasan tapak dan melayani pengguna di sekitarnya. **Jumlah pengguna terlayani** dihitung berdasarkan **cakupan radius pelayanan fasilitas** sesuai **SNI 03-1733-2004**. Perhitungan dilakukan dengan mengalikan jumlah unit bangunan terlayani dengan asumsi 4 jiwa per bangunan. Hasil perhitungan disajikan pada tabel berikut:

Fasilitas	Radius Pencapaian (m)	Jumlah Unit Bangunan Terlayani	Jumlah Pengguna Terlayani (Jiwa)
SD	1000	4089	16356
SMP	1000	4796	19184
SMA	3000	15197	60788
Kesehatan (Apotek, Praktek Dokter)	1500	7074	28296
Pertokoan	2000	9352	37408
Pemerintahan dan Pelayanan Umum	500	2625	10500
Masjid	1000	5271	21084
Gereja	1000	3695	14780
Ruang Terbuka Hijau	1000	3336	13.344
Pasar	5000	32283	129132

Carrying Capacity

Asumsi
1 jiwa = 10 m2 ; 1 KK = 4 jiwa

Fungsi Terbangun
17,035 ha (80%)

Ruang Terbangun
21,294 ha (60%)

Luas Tapak
35,49 ha

Ruang Non Terbangun
14,196 ha (40%)

Sirkulasi
4,258 ha (20%)

Carrying Capacity
170.350 m2 / 10 m2 = 17.035 jiwa = 4.337 KK

Kebutuhan Ruang & Perhitungan Gap Lahan

No	Kelompok Aktivitas	Jenis Ruang / Fasilitas	Pengguna	Standar Luas Lahan (SNI 03 / Data Spesifik)	Jml Unit Eksisting	Jml Unit Rencana	Total Kebutuhan Lahan (m^2)	Sumber & Keterangan Khusus
1	Permukiman	Hunian Tipe Sedang	Masyarakat lokal	120 m^2/kavling	146 unit	70 unit	8.400	Data asumsi dari tabel sebelumnya.
		Hunian Tipe Kecil	Masyarakat lokal	60 m^2/kavling	100 unit	180 unit	10.800	Data asumsi dari tabel sebelumnya.
2	Peribadatan	Musholla / Langgar	Masyarakat lokal	100 m^2/lokasi	-	4 unit	400	Standar 1/250 jiwa (butuh 39 unit). Dikompak-kan menjadi 4 unit besar karena lahan terbatas.
		Masjid Warga	Masyarakat lokal	600 m^2/lokasi	-	1 unit	600	Standar 1/2.500 jiwa.
3	Pendidikan	Taman Kanak-kanak (TK)	Anak usia dini	500 m^2/lokasi	-	2 unit	1.000	Standar 1/1.250 jiwa. (Butuh 8 unit, dibuat 2 unit besar).
		SD / MI	Anak 7-12 th	2.000 m^2/lokasi	1 unit	1 unit	2.000	Standar 1/1.600 jiwa. (Butuh 6 unit, eksisting 1 + rencana 1).
		SLTP / MTs	Remaja 13-15 th	9.000 m^2/lokasi	1 unit	1 unit	9.000	Standar 1/4.800 jiwa. (Butuh 2 unit, eksisting 1 + rencana 1).
4	Kesehatan	Posyandu	Balita & Ibu	60 m^2/lokasi	-	4 unit	240	Standar 1/1.250 jiwa. (Butuh 8 unit, dibuat 4 unit).
		Balai Pengobatan Warga	Masyarakat umum	300 m^2/lokasi	-	1 unit	300	Standar 1/2.500 jiwa.
		Puskesmas Pembantu (Pustu)	Masyarakat umum	300 m^2/lokasi	-	1 unit	300	Standar 1/30.000 jiwa, 1 unit sudah cukup.
5	Pemerintahan & Pelayanan Umum	Balai Pertemuan Warga	Masyarakat & Aparat	300 m^2/lokasi	1 unit	1 unit	300	1 per RW (ada 4 RW), bisa diintegrasikan.
		Kantor Kelurahan / Desa	Perangkat Desa	1.000 m^2/lokasi	-	1 unit	1.000	Pengganti Kantor Kecamatan (karena di skala desa).
		Pos Keamanan (Hansip/Kamtib)	Keamanan	200 m^2/lokasi	-	1 unit	200	Standar SNI untuk skala kelurahan.
		Pos Pemadam Kebakaran	Masyarakat	1.000 m^2/lokasi	1 unit	1 unit	1.000	Data dari tabel gambar Anda.
		Bawaslu (Pengawas Pemilu)	Aparat	300 m^2/lokasi	1 unit	1 unit	300	Data dari tabel gambar Anda.
		Balai Penyuluhan KB	Masyarakat	300 m^2/lokasi	1 unit	1 unit	300	Data dari tabel gambar Anda.

Kebutuhan Ruang & Perhitungan Gap Lahan

No	Kelompok Aktivitas	Jenis Ruang / Fasilitas	Pengguna	Standar Luas Lahan (SNI 03 / Data Spesifik)	Jml Unit Eksisting	Jml Unit Rencana	Total Kebutuhan Lahan (m^2)	Sumber & Keterangan Khusus
6	Perdagangan & Jasa (Lokal)	Toko / Warung Kelontong	Masyarakat setempat	100 m^2/lokasi	-	39 unit	3.900	Standar 1/250 jiwa. (9.694/250 = 38,8).
		Pertokoan (Skala Sub-Lingkungan)	Masyarakat	3.000 m^2/lokasi	-	1 unit	3.000	Standar 1/6.000 jiwa.
7	Distribusi & Logistik Pasar	Parkir Truk / Loading Bay	Pedagang Pasar, Supir Logistik	30 m^2/lot truk (Estimasi 80 truk dari 1.616 pedagang)	-	80 lot	2.400	WAJIB. Mengatasi aktivitas bongkar muat yang selama ini di bahu jalan.
8	Rekreasi & Olahraga	Taman / Tempat Bermain	Masyarakat umum	250 m^2/lokasi	-	4 unit	1.000	Standar 1/250 jiwa. Direncanakan 4 taman tersebar.
		Lapangan Olahraga Serbaguna	Masyarakat umum	9.000 m^2/lokasi	-	1 unit	9.000	Standar 1/30.000 jiwa, 1 unit untuk skala desa sudah cukup.
9	Transportasi & Parkir	Parkir Umum (Pusat Kegiatan)	Pengunjung & Masyarakat	1.000 m^2/lokasi	-	1 unit	1.000	Ditingkatkan dari 500 m^2 karena adanya Pasar Induk.
		Parkir Motor (Khusus Wisata)	Wisatawan & Masyarakat	2,7 m^2/lot (Standar Neufert)	-	250 lot	675	Data dari tabel gambar Anda.
		Parkir Mobil (Khusus Wisata)	Wisatawan & Masyarakat	4,7 m^2/lot (Standar Neufert)	-	50 lot	235	Data dari tabel gambar Anda.
		Holding Area (Ruang Tunggu)	Kendaraan R4 & R2	Perlintasan sebidang wajib memiliki ruang tunggu minimal 15 m dari palang pintu.	-	1 paket (50m x 4m)	200	WAJIB. Mengatasi kemacetan akibat antrean kereta api di Jl. A.Yani.
10	Persampahan	TPS (Tempat Pembuangan Sementara)	Masyarakat	Menyesuaikan (≈ 6 m^3)	-	4 unit	-	1 TPS per RW (4 RW). Lokasi bebas, minimal 30m dari pemukiman.
TOTAL KEBUTUHAN LAHAN (m^2)	**57.550**							

Hubungan Antar-Kelompok Aktivitas

Kelompok Aktivitas	Hunian	Perdagangan	Transportasi	Distribusi
Hunian	—	**Kuat** – masyarakat menjadi pengguna aktivitas perdagangan, sementara beberapa hunian juga berkembang dengan fungsi ekonomi seperti warung makan dan usaha rumahan.	**Kuat** – hunian berkembang mengikuti koridor transportasi dan membutuhkan akses untuk mendukung mobilitas masyarakat.	**Sedang** – kebutuhan masyarakat terhadap barang dari aktivitas perdagangan didukung oleh aktivitas distribusi.
Perdagangan	**Kuat** – permukiman di sekitar kawasan menjadi konsumen sekaligus mendukung aktivitas ekonomi perdagangan.	—	**Sangat kuat** – aktivitas perdagangan membutuhkan transportasi untuk mobilitas pedagang, pembeli, dan barang.	**Sangat kuat** – perdagangan bergantung pada distribusi barang, sementara aktivitas distribusi mendukung ketersediaan barang di pasar.
Transportasi	**Kuat** – menjadi pendukung mobilitas masyarakat dari dan menuju hunian.	**Sangat kuat** – tingginya aktivitas perdagangan meningkatkan pergerakan kendaraan menuju kawasan pasar.	—	**Sangat kuat** – jaringan transportasi menjadi prasarana utama perpindahan barang menuju dan dari Pasar Induk Kroya.
Distribusi	**Sedang** – distribusi mendukung pemenuhan kebutuhan barang bagi masyarakat di kawasan hunian.	**Sangat kuat** – Pasar Induk Kroya menjadi pusat perdagangan sekaligus distribusi barang bagi wilayah Kroya dan sekitarnya.	**Sangat kuat** – aktivitas distribusi bergantung pada konektivitas jaringan jalan untuk pergerakan barang.	—

Organisasi Ruang Kawasan

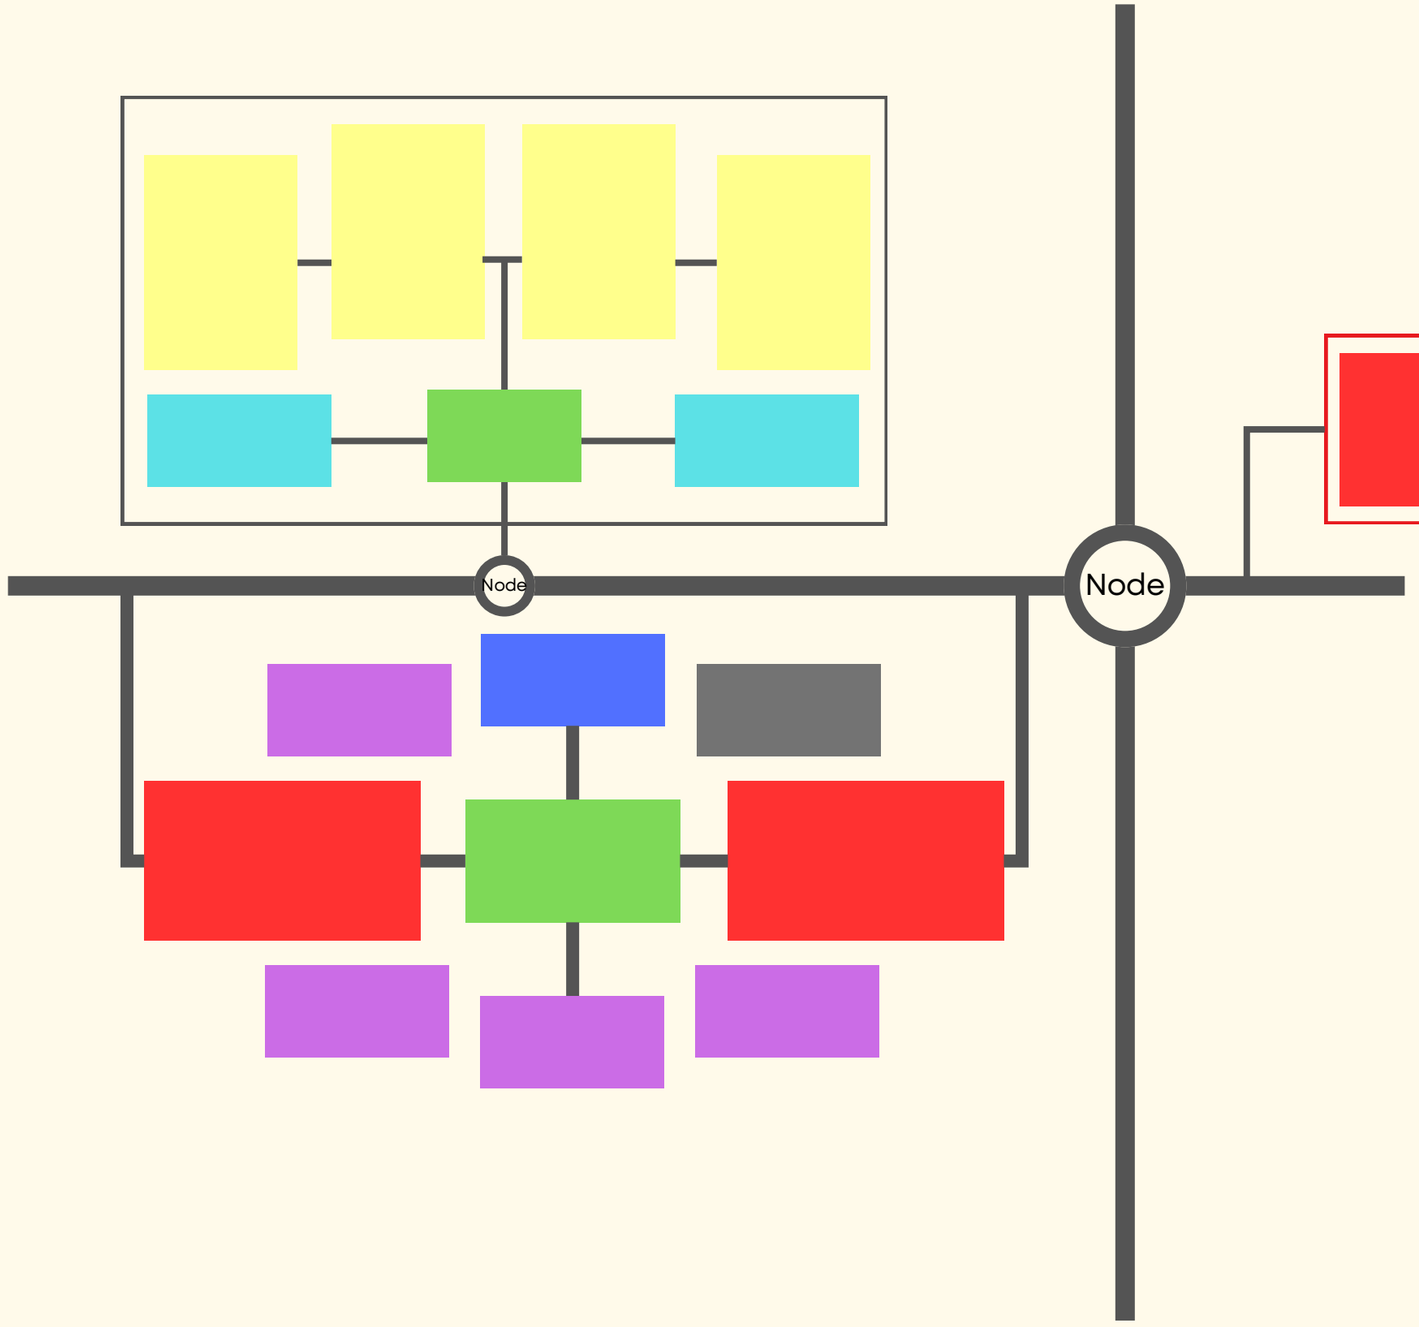

LEGENDA

- Enterance Gate
- Hunian
- Pendidikan
- Pergantian Moda
- Parkir Sepeda/ Lot
- Ruang Terbuka Hijau
- Perdagangan dan Jasa
- Fasilitas Pelayanan Umum
- Pasar

Bab II

ANALISIS FISIK (ANALISIS SITE)

Lingkungan

Data

- Lahan terbangun mencapai 70,2% dari luas tapak dengan RTH yang sangat terbatas. kawasan dibatasi badan air (sungai) di sisi utara sesuai delineasi. aktivitas Pasar Induk Kroya (1.616 pedagang) dan simpang rel KA sebagai titik konsentrasi sampah dan emisi kendaraan.

Analisis

- Rendahnya proporsi RTH terhadap lahan terbangun mengindikasikan minimnya daya dukung lingkungan untuk menyerap polutan udara dan air limpasan. mangkraknya revitalisasi Pasar Induk Kroya (M2) berisiko menghasilkan limbah padat/cair tanpa penanganan memadai. kepadatan lalu lintas di simpang rel - Jl. A. Yani (M1) menjadi sumber emisi terkonsentrasi.

Respon

- Mengalokasikan RTH/taman (sudah direncanakan 4 unit @250 m^2 pada tabel kebutuhan ruang) sekaligus sebagai zona penyangga lingkungan. menyediakan TPS dengan pemilahan sampah untuk aktivitas pasar (4 unit, sudah ada di tabel). vegetasi penyerap polutan mengikuti daftar yang sudah Anda tulis di Respon Vegetasi.

Topografi

Data

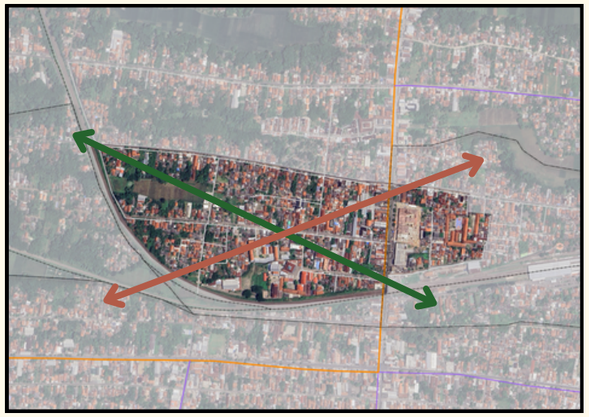

Garis Vertikal

Kontur dari garis vertikal sepanjang ... km memiliki interval sebesar ... dengan karakteristik .....

Garis Horizontal

Kontur dari garis horizontal sepanjang ... km memiliki interval sebesar ... dengan karakteristik .....

Analisis

Berdasarkan data DEMNAS, topografi kawasan perencanaan berada pada ketinggian 107-145 mdpl.

- Vertikal = ((jumlah kontur+1) X Kontur Interval) X 100%/ panjang garis potong
  =((10+1)X 5) X 100%/ 1176
  = 4,67%
- Horizontal = (jumlah kontur+1) X Kontur Interval X 100%/ panjang garis potong
  = ((8+1)X 5) X 100%/ 1301
  = 3,45%
- Berdasarkan **PERMEN PU No. 41/PRT/M/2007** Tingkat kemiringan lereng yang aman untuk dijadikan kawasan indutri yaitu **0-25%.**
- Berdasarkan **SNI-03-1744-2004** kawasan permukiman sebaiknya ditempatkan di kawasan dengan tingkat kemiringan lereng **4-25%.**

Respon

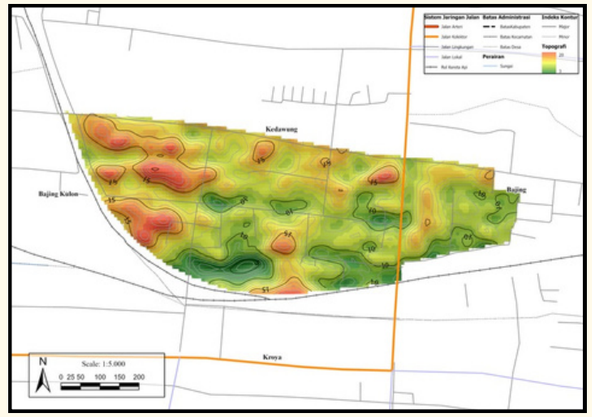

- Kawasan Perencanaan didominasi oleh kemiringan lereng yang **relatif landai yaitu 0-25%**
- Dengan ketinggian tersebut, **area lahan terbangun eksisting sudah cukup baik**. Pola bangunan terlihat tidak beraturan.
- Kawasan Industri lebih baik diletakkan pada area dengan **garis kontur yang renggang** sehingga akan mempermudah distribusi.
- Kawasan Pertanian lebih baik diletakkan pada area dengan **garis kontur yang lebih rapa**t untuk memudahkan fungsi irigasi.

Drainase

Data

- xxx

Analisis

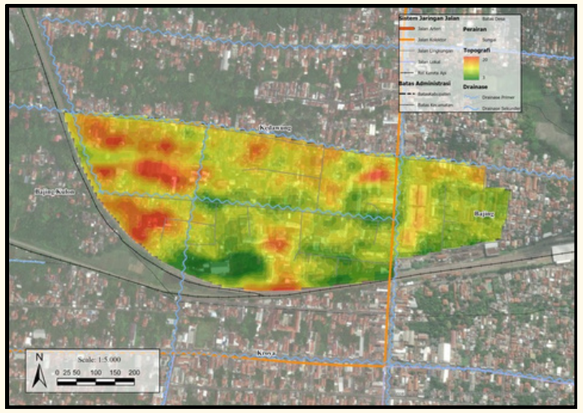

- xxx

Respon

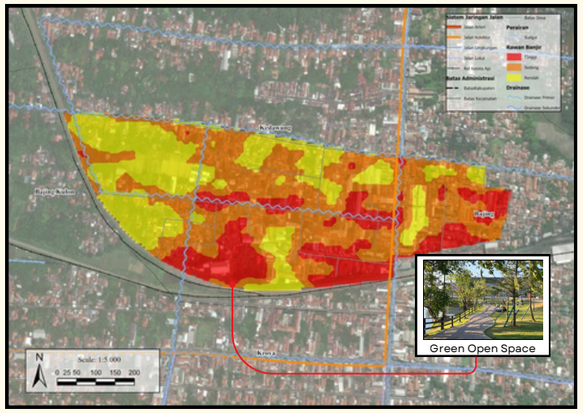

- xxx

Aksesibilitas

Data

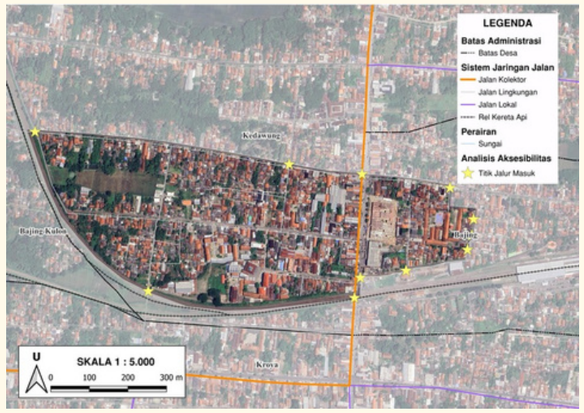

- Kawasan tapak kecamatan Kroya terdapat **11 akses keluar masuk**
- Kawasan dilintasi dengan Jalan Kolektor Primer yaitu Jalan Jendral Ahmad Yani yang **terhubung dengan Jalan Arteri** di utara Kecamatan Kroya.
- Kawasan juga terkoneksi dengan **jalan lokal dan lingkungan** yang **menghubungkan permukiman dengan pusat kegiatan** yaitu Pasar Induk Kroya.

Analisis

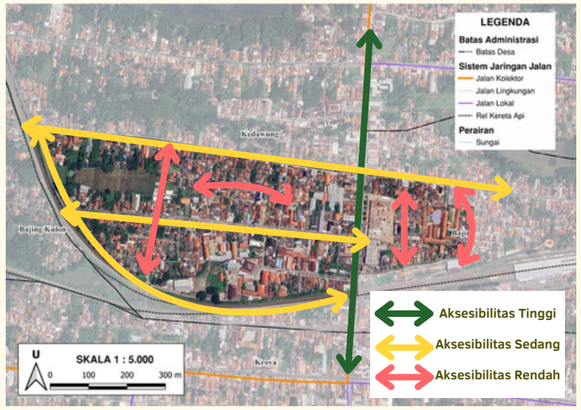

- Jalan Jendral Ahmad Yani digunakan sebagai **akses distribusi barang dan pergerakan manusia** sehingga perannya sangat penting bagi perekonomian kawasan.
- Terdapat **persimpangan rel kereta api yang menghambat distribusi barang** karena letaknya yang dekat dengan Pasar Induk Kroya sehingga sering terjadi kemacetan.
- Kondisi jalan lokal dan lingkungan cenderung **tidak terlalu lebar** yang hanya bisa dilintasi maksimal 2 mobil dan belum difasilitasi dengan trotoar.

Respon

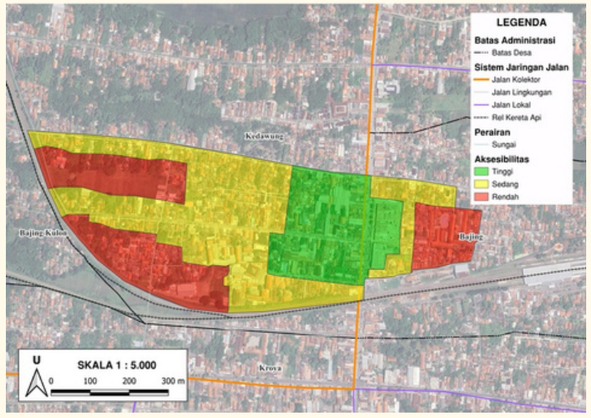

- **Jalan Jenderal Ahmad Yani** digunakan sebagai **jalan utama dan main entrance** karena terhubung dengan Jalan Arteri di utara
- Perlu ada **peningkatan kualitas** jalan yang ada seperti **memperbaiki jalan dan menambahkan jalur pedestrian** yang memadai agar meningkatkan kesadaran berjalan kaki.
- Perlu ada **rekayasa lalu lintas pada jam-jam tertentu** (pagi dan sore) untuk meredam kemacetan di persimpangan rel kereta api agar pergerakan tidak terhambat

Kebisingan

Data

- Data: 147 perjalanan KA/hari melintasi perlintasan sebidang dekat pasar (M1). kemacetan berulang di Jl. Jenderal Ahmad Yani. aktivitas bongkar-muat Pasar Induk Kroya.

Analisis

- Analisis: Berdasarkan Kepmen LH No. 48/1996, ambang kebisingan kawasan perdagangan & jasa (70 dB) jauh lebih longgar dari kawasan permukiman (55 dB) karena hunian di kawasan ini berkembang linear berdampingan langsung dengan koridor pasar dan rel (sudah tercatat di slide Hunian/Karakteristik Aktivitas), kebisingan yang "wajar" untuk zona komersial berpotensi melebihi baku mutu permukiman di sisi hunian yang berbatasan langsung.

Respon

- Respon: Jalur vegetasi peredam sepanjang koridor rel dan Jl. A. Yani (beringin, bambu kuning, trembesi, kayu putih). ruang tunggu/holding area kendaraan di perlintasan (sudah direncanakan 50×4 m) sekaligus berfungsi sebagai jarak penyangga. Angka dB spesifik sebaiknya diisi dari pengukuran sound level meter lapangan.

View

Data

View from site

1. Persawahan di luar kawasan
2. Perbukitan di Kab. Banyumas
3. Hutan bambu

View to site

1. Persawahan di dalam kawasan
2. Rel Kereta Api

Analisis

View from site

1 2 3

Persawahan **memperkuat karakter agrari**s kawasan, sedangkan hutan bambu membentuk **batas visual alami**. Perbukitan di kejauhan berpotensi sebagai **latar visual**, namun belum terlalu dominan.

View to site

1 2

Hamparan sawah eksisting membentuk **citra alami** tapak, sementara rel kereta menjadi elemen linier yang **memperkuat karakter kawasan sekitar.**

Respon

1. View perbukitan dapat dimanfaatkan sebagai **orientasi visual kawasan** melalui koridor pandang strategis.
2. Hutan bambu berpotensi dipertahankan sebagai **buffer hijau alami** yang memperkuat kualitas visual kawasan.
3. Persawahan dapat dipertahankan sebagai **ruang terbuka** yang menjaga karakter agraris kawasan.
4. Rel kereta memiliki potensi sebagai **elemen identitas** kawasan melalui penataan tepi yang teratur.

Arah Angin & Orientasi Matahari

Data

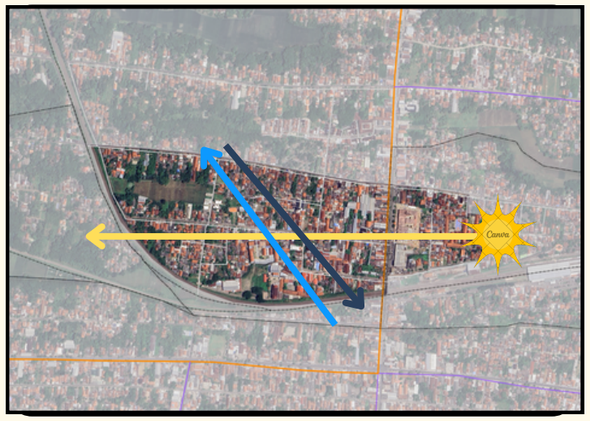

Keterangan:
- Arah Cahaya Matahari
- Arah Angin Siang Hari
- Arah Angin Malam Hari

- **Arah cahaya matahari** dari arah timur ke barat melalui kawasan tapak.
- **Arah angin** bergerak dari dataran rendah menuju dataran tinggi (tenggara ke barat laut) pada siang hari dan sebaliknya pada malam hari.
- Rata-rata **suhu udara** pada kawasan tapak adalah **26 - 30°C** (BMKG)
- Lama durasi matahari berkisar **12 jam 10 menit** (05.48 - 17.58).

Analisis

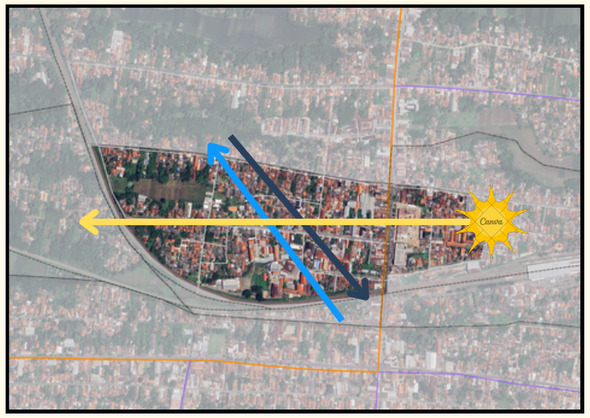

Keterangan:
- Arah Cahaya Matahari
- Arah Angin Siang Hari
- Arah Angin Malam Hari

- Lintasan matahari dan arah angin dapat dijadikan **faktor penentu orientasi arah bangunan**.
- Bangunan yang menghadap timur/barat di kawasan tapak cenderung **terpapar langsung** oleh sinar matahari karena searah dengan lintasannya.
- Banyaknya vegetasi menjadikannya sebagai ***barrier* alami** agar cahaya matahari tidak menyinari secara langsung.

Respon

Keterangan:
- Arah Cahaya Matahari
- Arah Angin Siang Hari
- Arah Angin Malam Hari
- Sumbu Ideal

- **Garis sumbu ideal** menentukan orientasi bangunan. Dimana lebih baik untuk menghadap **arah timur** laut dan **barat daya**, sehingga lebih **optimal** dalam memperoleh pencahayaan dan **sirkulasi udara**.
- Pada desain bangunan yang menghadap arah timur dan barat dibutuhkan **elemen peneduh** agar mengurangi intensitas cahaya matahari.

Vegetasi

Data

- **Vegetasi** terdiri dari **padi, kelapa, mangga pisang, bambu, singkong, dan glodokan** yang tersebar di pekarangan dan tepi jalan.
- Kawasan didominasi oleh **lahan terbangun** mencapai **70,2%** dari total luas kawasan, sehingga **vegetasi** dalam kawasan **terbatas**.
- **Tidak tersedianya** vegetasi di sepanjang jalan kolektor.
- Tidak terdapat Ruang Terbuka Hijau (RTH) untuk **rekreasi masyarakat** di kawasan.

Analisis

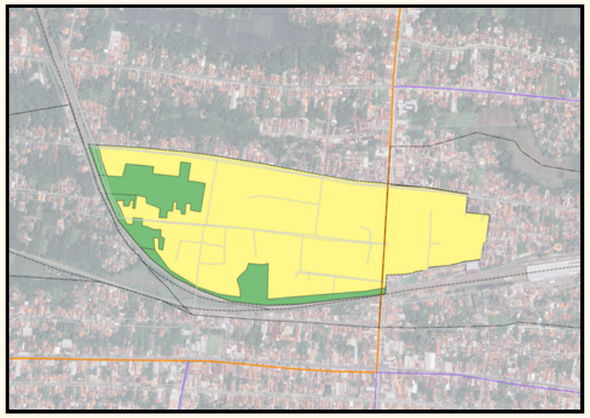

- **Penanaman vegetasi** pada jalan kolektor dan jalan lokal berfungsi untuk **meminimalisir udara kotor**, sebagai **estetika**, dan **meningkatkan kualitas lingkungan hidup.**
- Menurut pendapat **Rustam Hakim (2002),** fungsi tanaman dikategorikan sebagai berikut :
  1. **kontrol pandangan**
  2. **pembatas fisik**
  3. **pengendali iklim**
  4. **pencegah erosi**
  5. **habitat satwa**
  6. **nilai estetis**
- Hannebaum (1981) dalam *Landscape Design* menyebutkan bahwa dalam peletakan tanaman harus **mempertimbangkan variasi, penekanan, keseimbangan. kesedarhanaan, dan keurutan.**

Respon

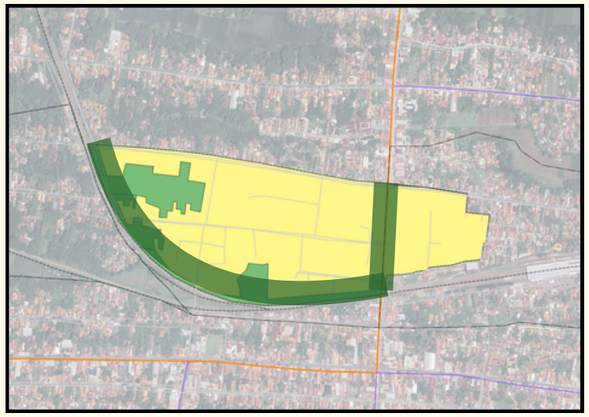

Memberikan **koridor hijau** atau **pepohonan peneduh** di sepanjang jalan utama untuk meningkatkan **kenyamanan** dan **kualitas** lingkungan serta peletakan tanaman penyerap air hujan di beberapa titik rawan genangan.

Pohon penahan kebisingan:
- (*ficus benjamina*) pohon beringin
- (*bambusa vulgaris*) bambu kuning
- (*samanea saman*) pohon trembesi
- (*melaleuca cajuputi*) pohon kayu putih

Pohon untuk daerah rawan genangan:
- Rumput Vetiver (Akar Wangi)
- *Canna* (Bunga Tasbih)
- *Cyperus* (Rumput Payung)
- Ketapang Kencana
- Jambu Air

TERIMA KASIH